

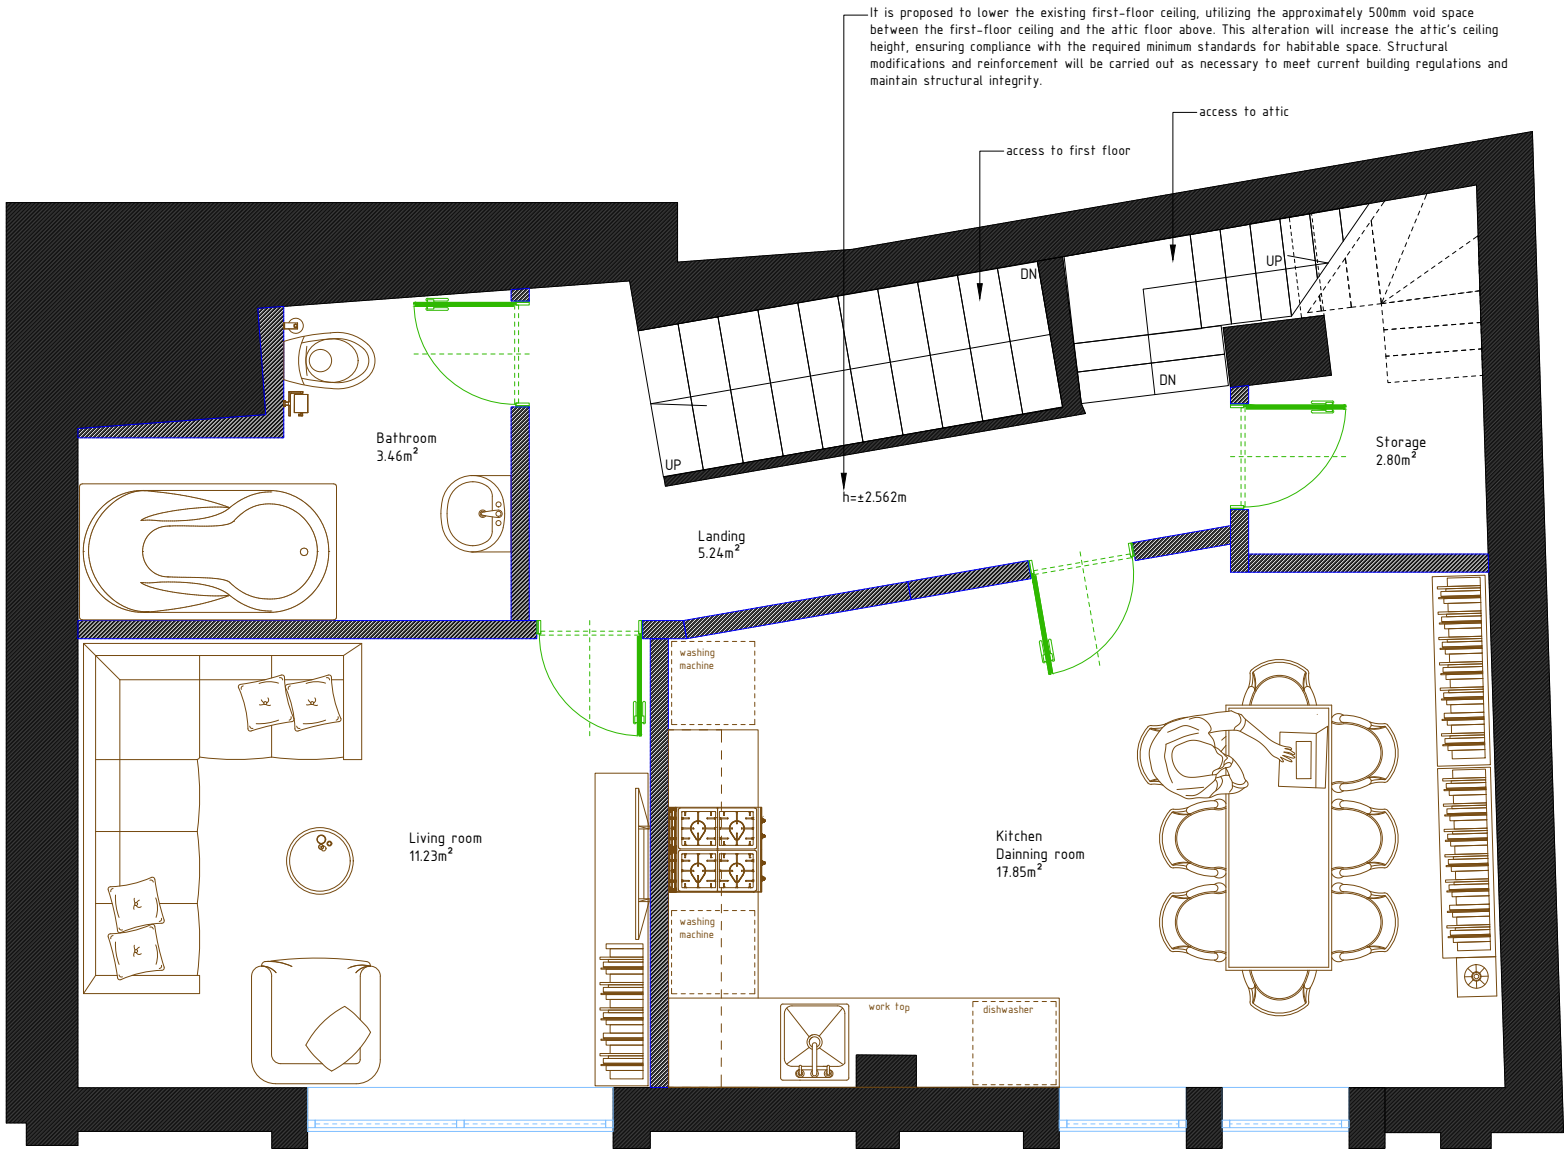
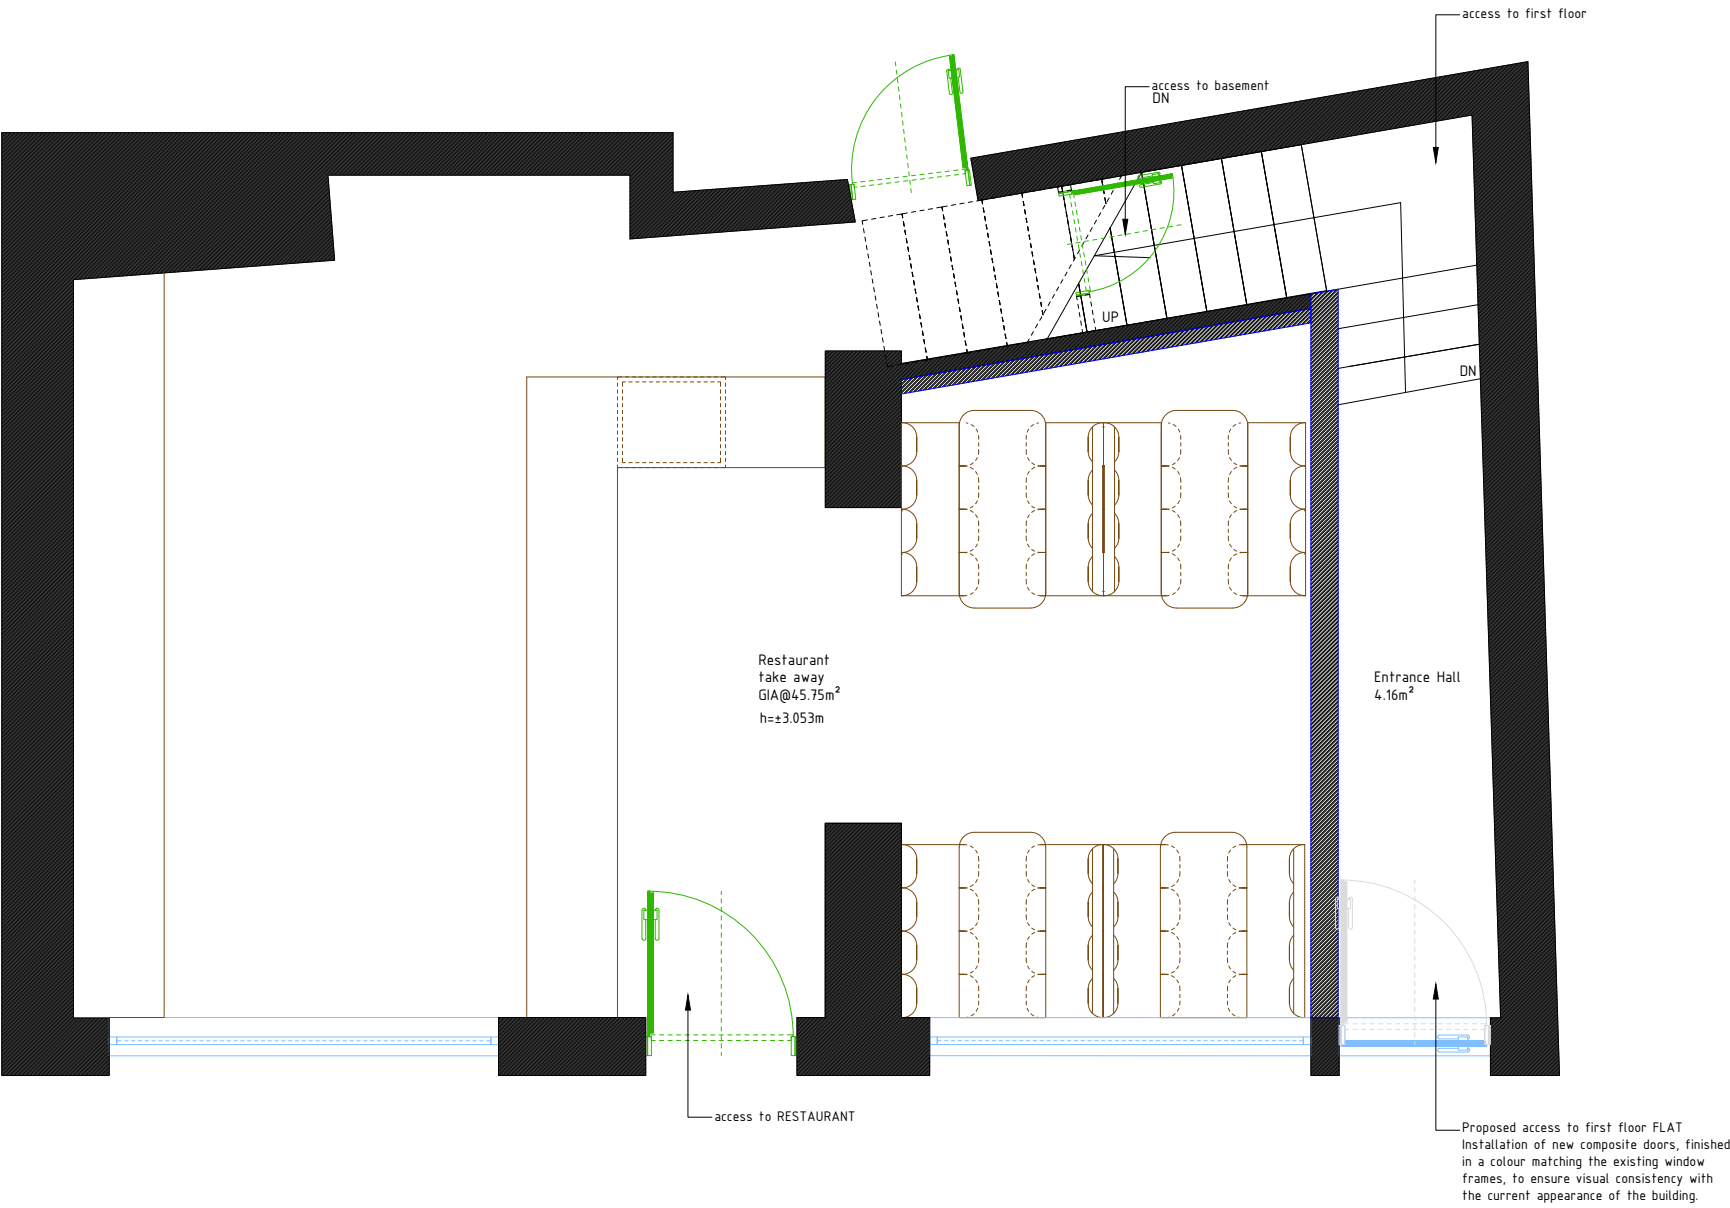


P_r PROPOSED floor plan 1:50@A2

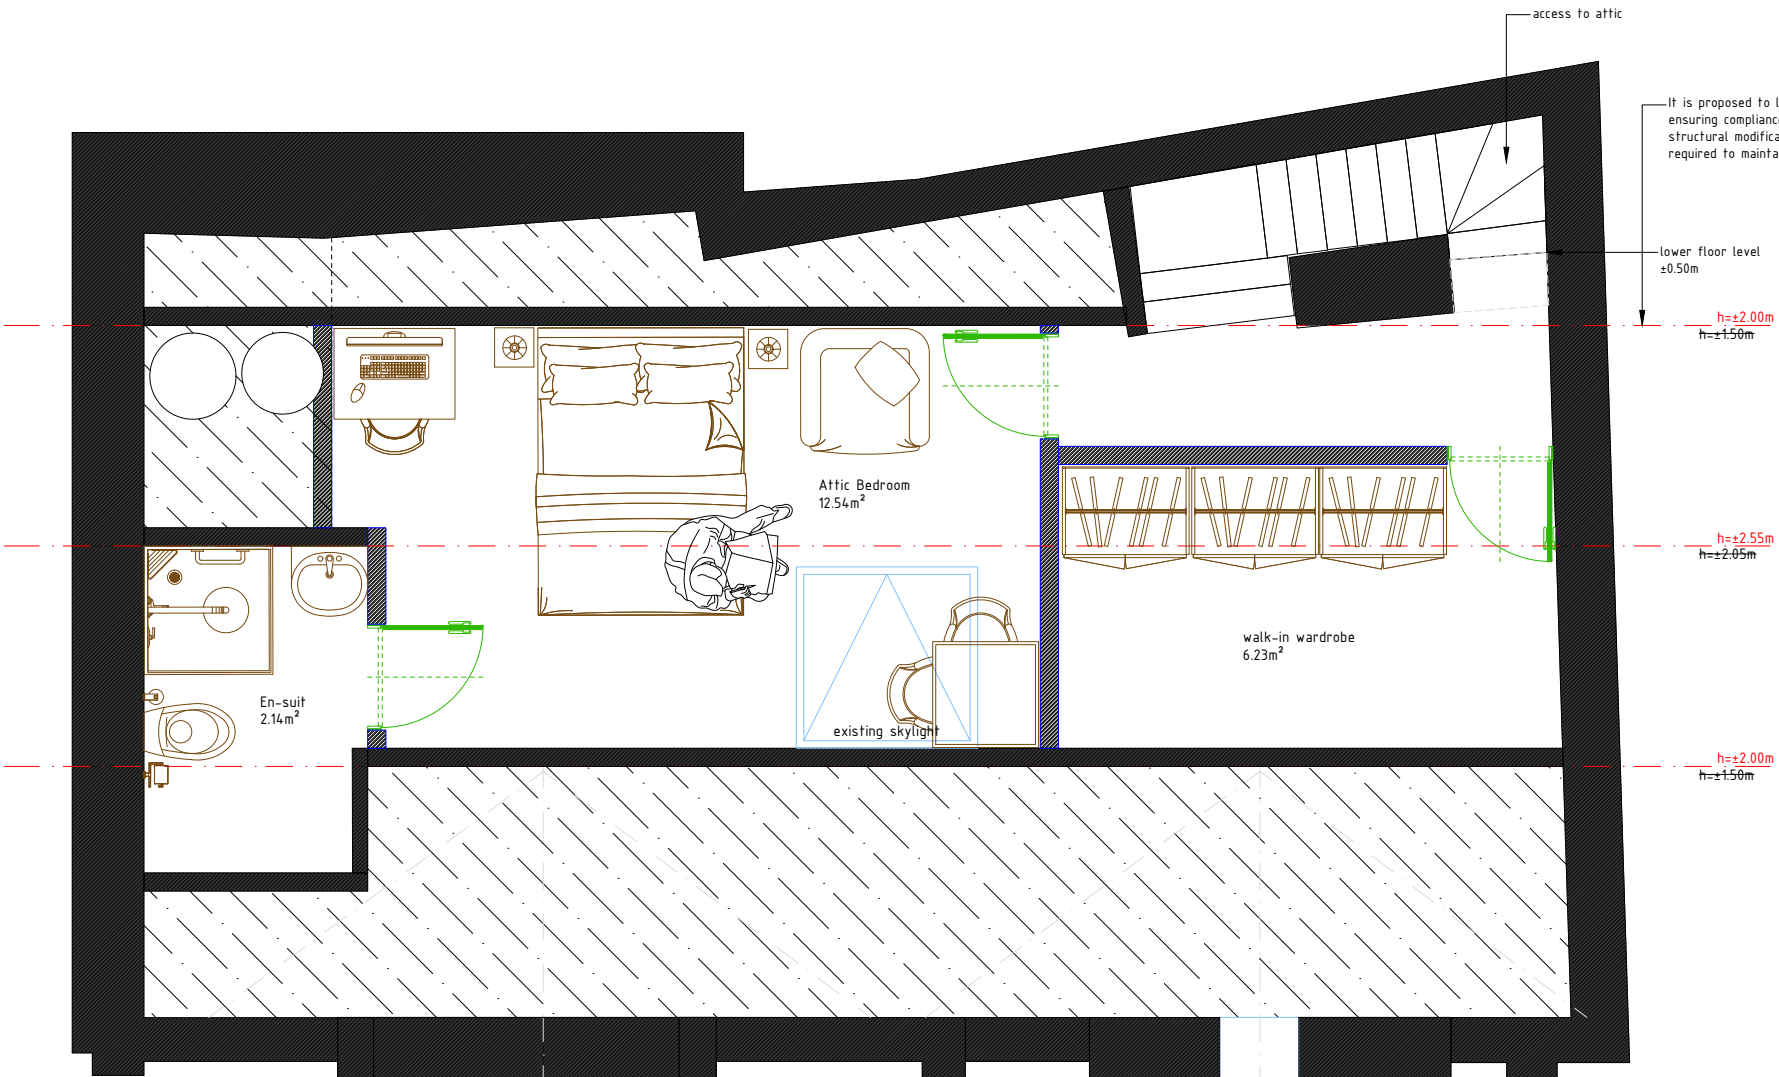

First floor and Attic flat

FIRST FLOOR	
Entrance Hall	4.16m ²
Landing	5.24m ²
Bathroom	3.46m ²
Living room	11.23m ²
Kitchen/Dining Room	17.85m ²
Storage	2.80m ²
ATTIC	
Attic Bedroom	12.54m ²
walk-in wardrobe	6.23m ²
En-suit	2.14m ²
Combined Total:	GIA @ 65.73m ²
(First Floor + Attic)	

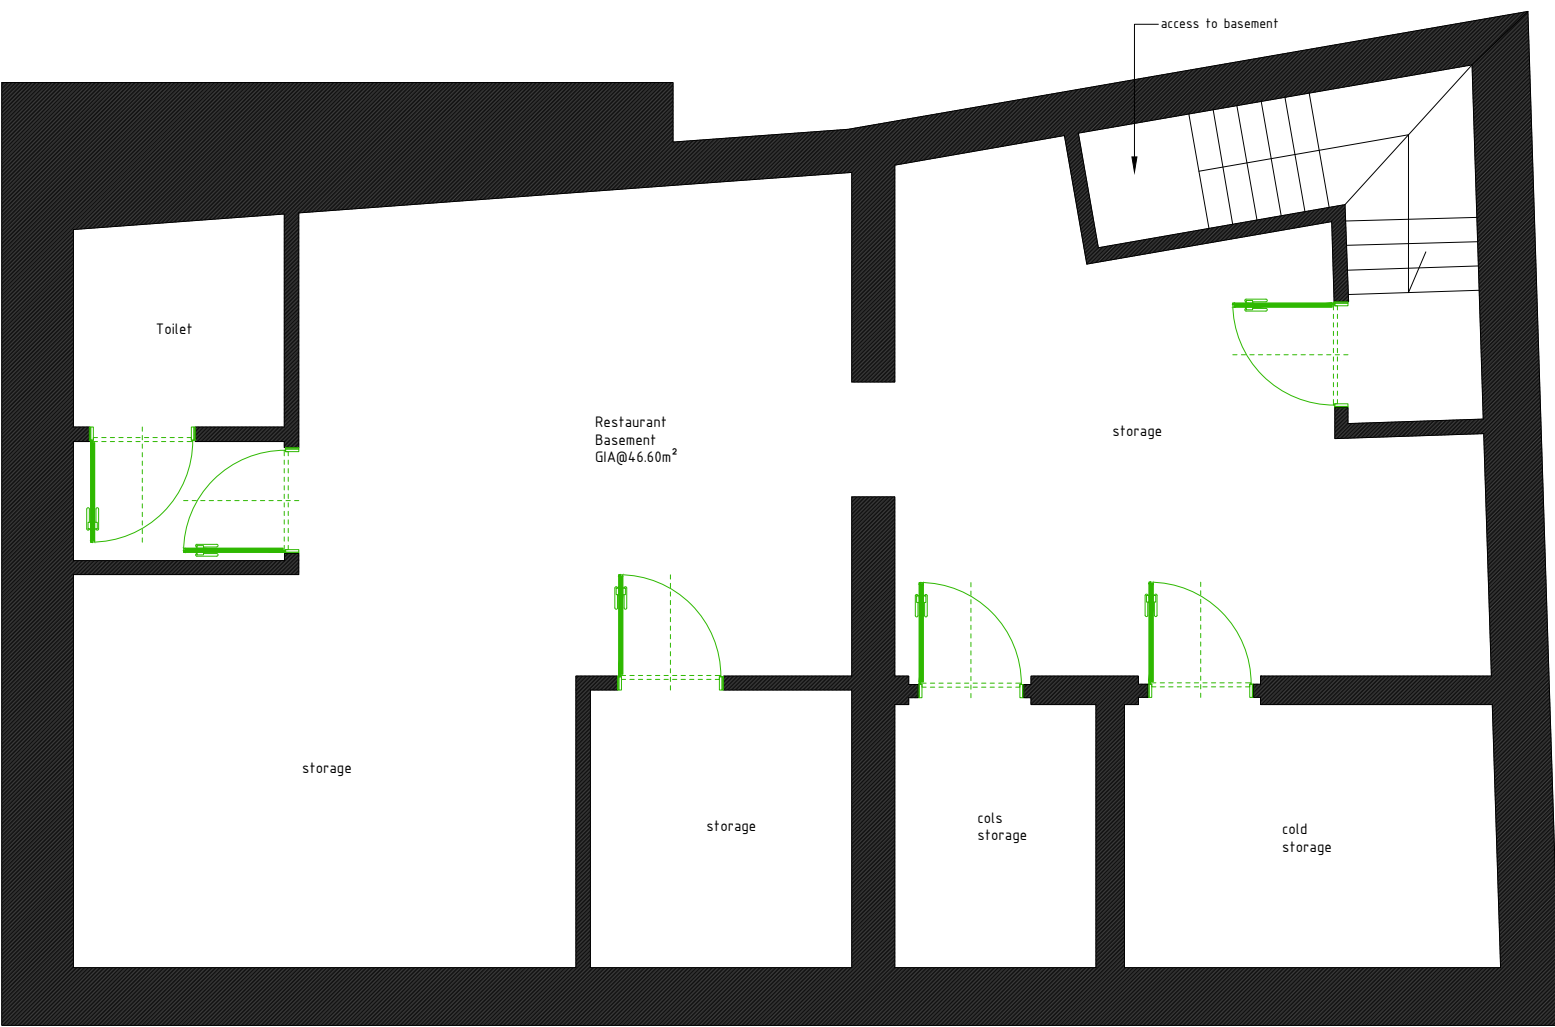

all dimension to be site checked by the constructor prior to procuring the materials and the site works etc. Temporary props to be designed and maintained by the contractor.

Notice: for building regulation submission only, not for ordering materials. Principal Contractors is responsible for taking measurements on site, prepare construction drawings and safety erecting the proposed structural works.