




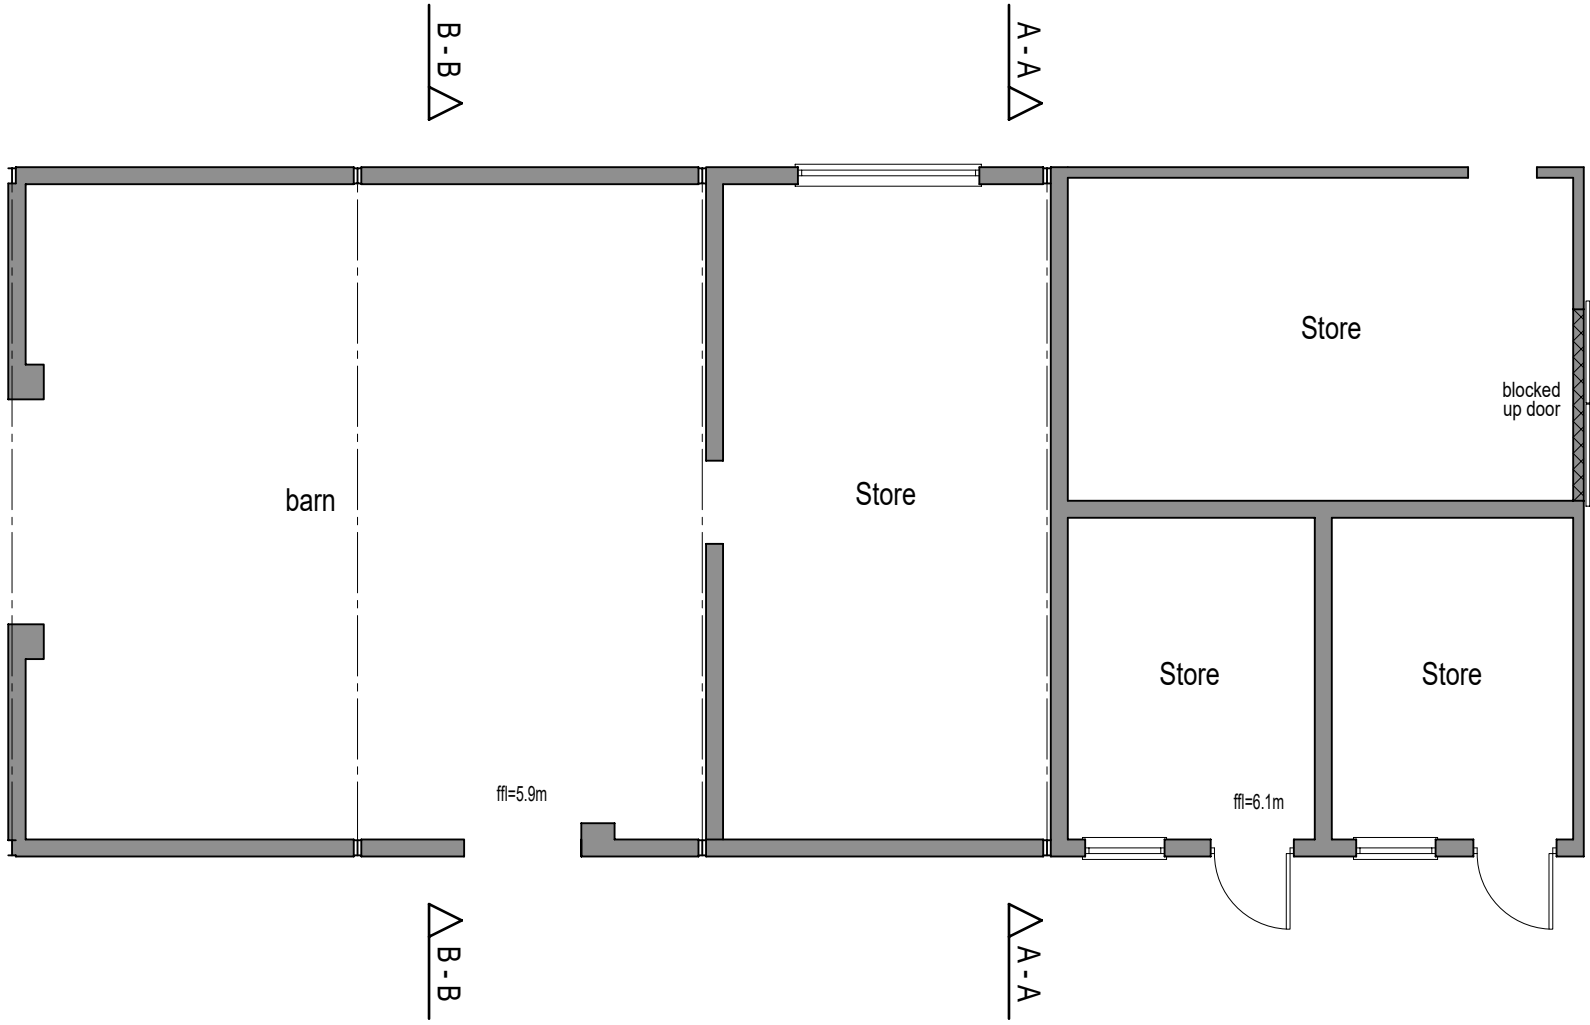


PROPOSED GROUND FLOOR PLAN
1:100

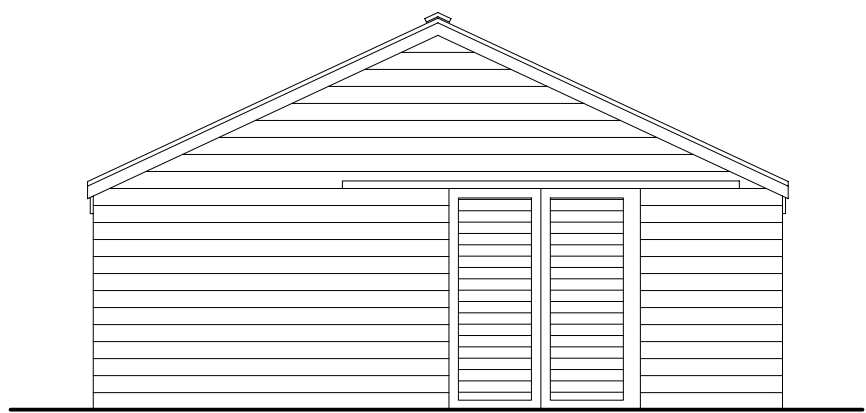


PROPOSED NORTH ELEVATION
1:100

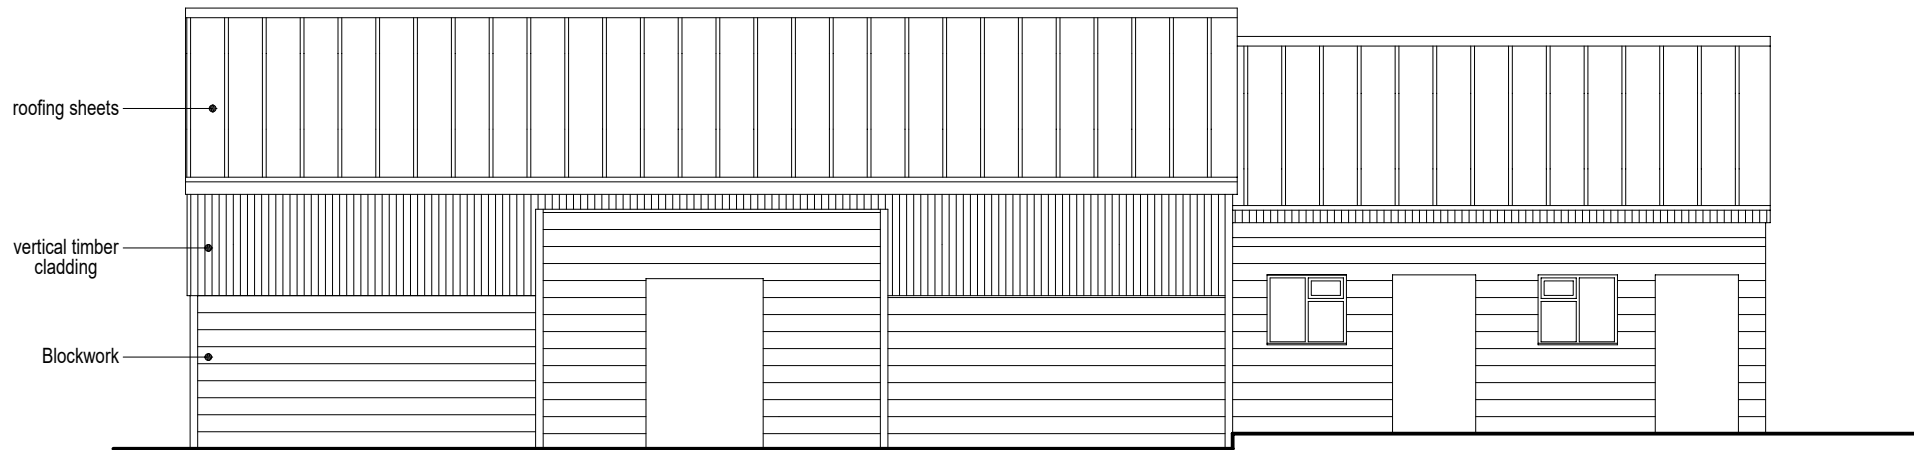


PROPOSED EAST ELEVATION

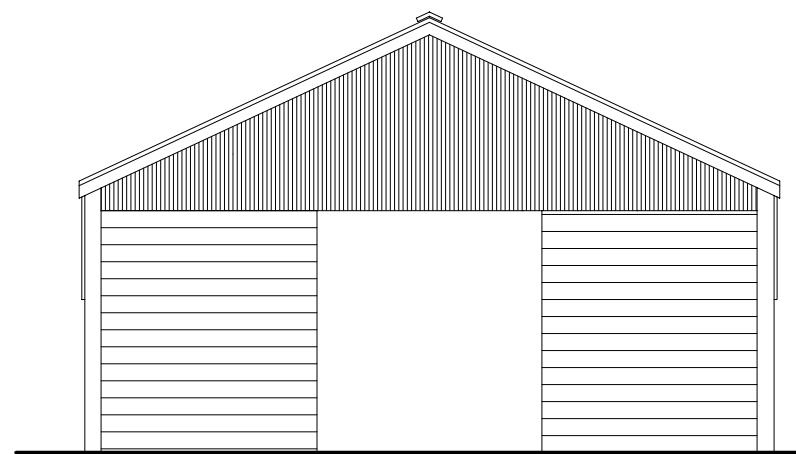


PROPOSED SOUTH ELEVATION

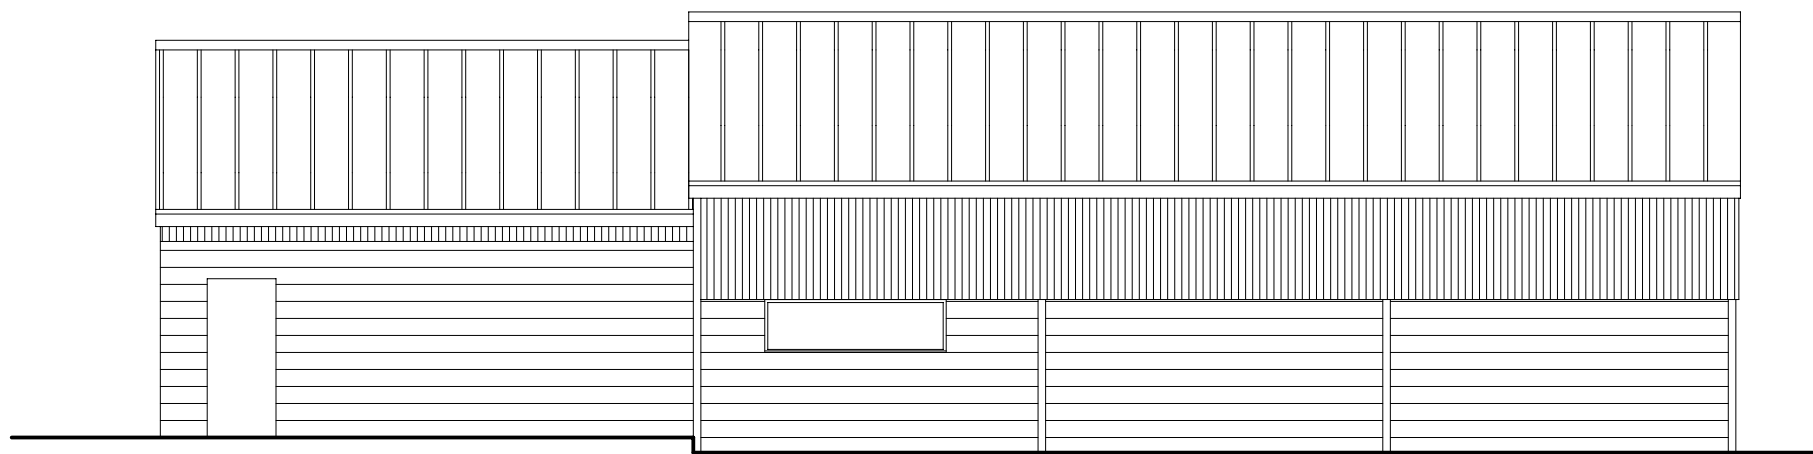



PROPOSED WEST ELEVATION

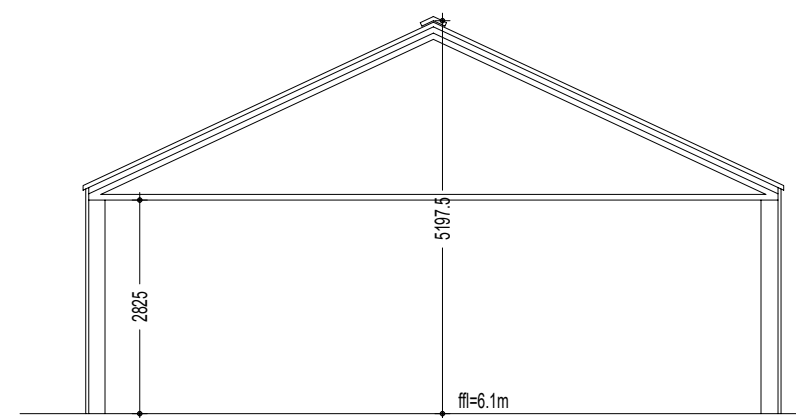


PROPOSED SECTION A - A
1:100

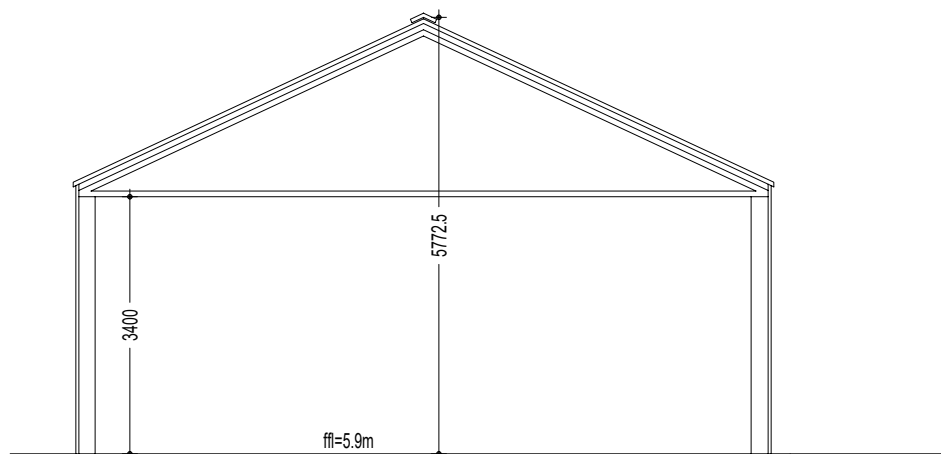

PROPOSED SECTION B - B
1:100

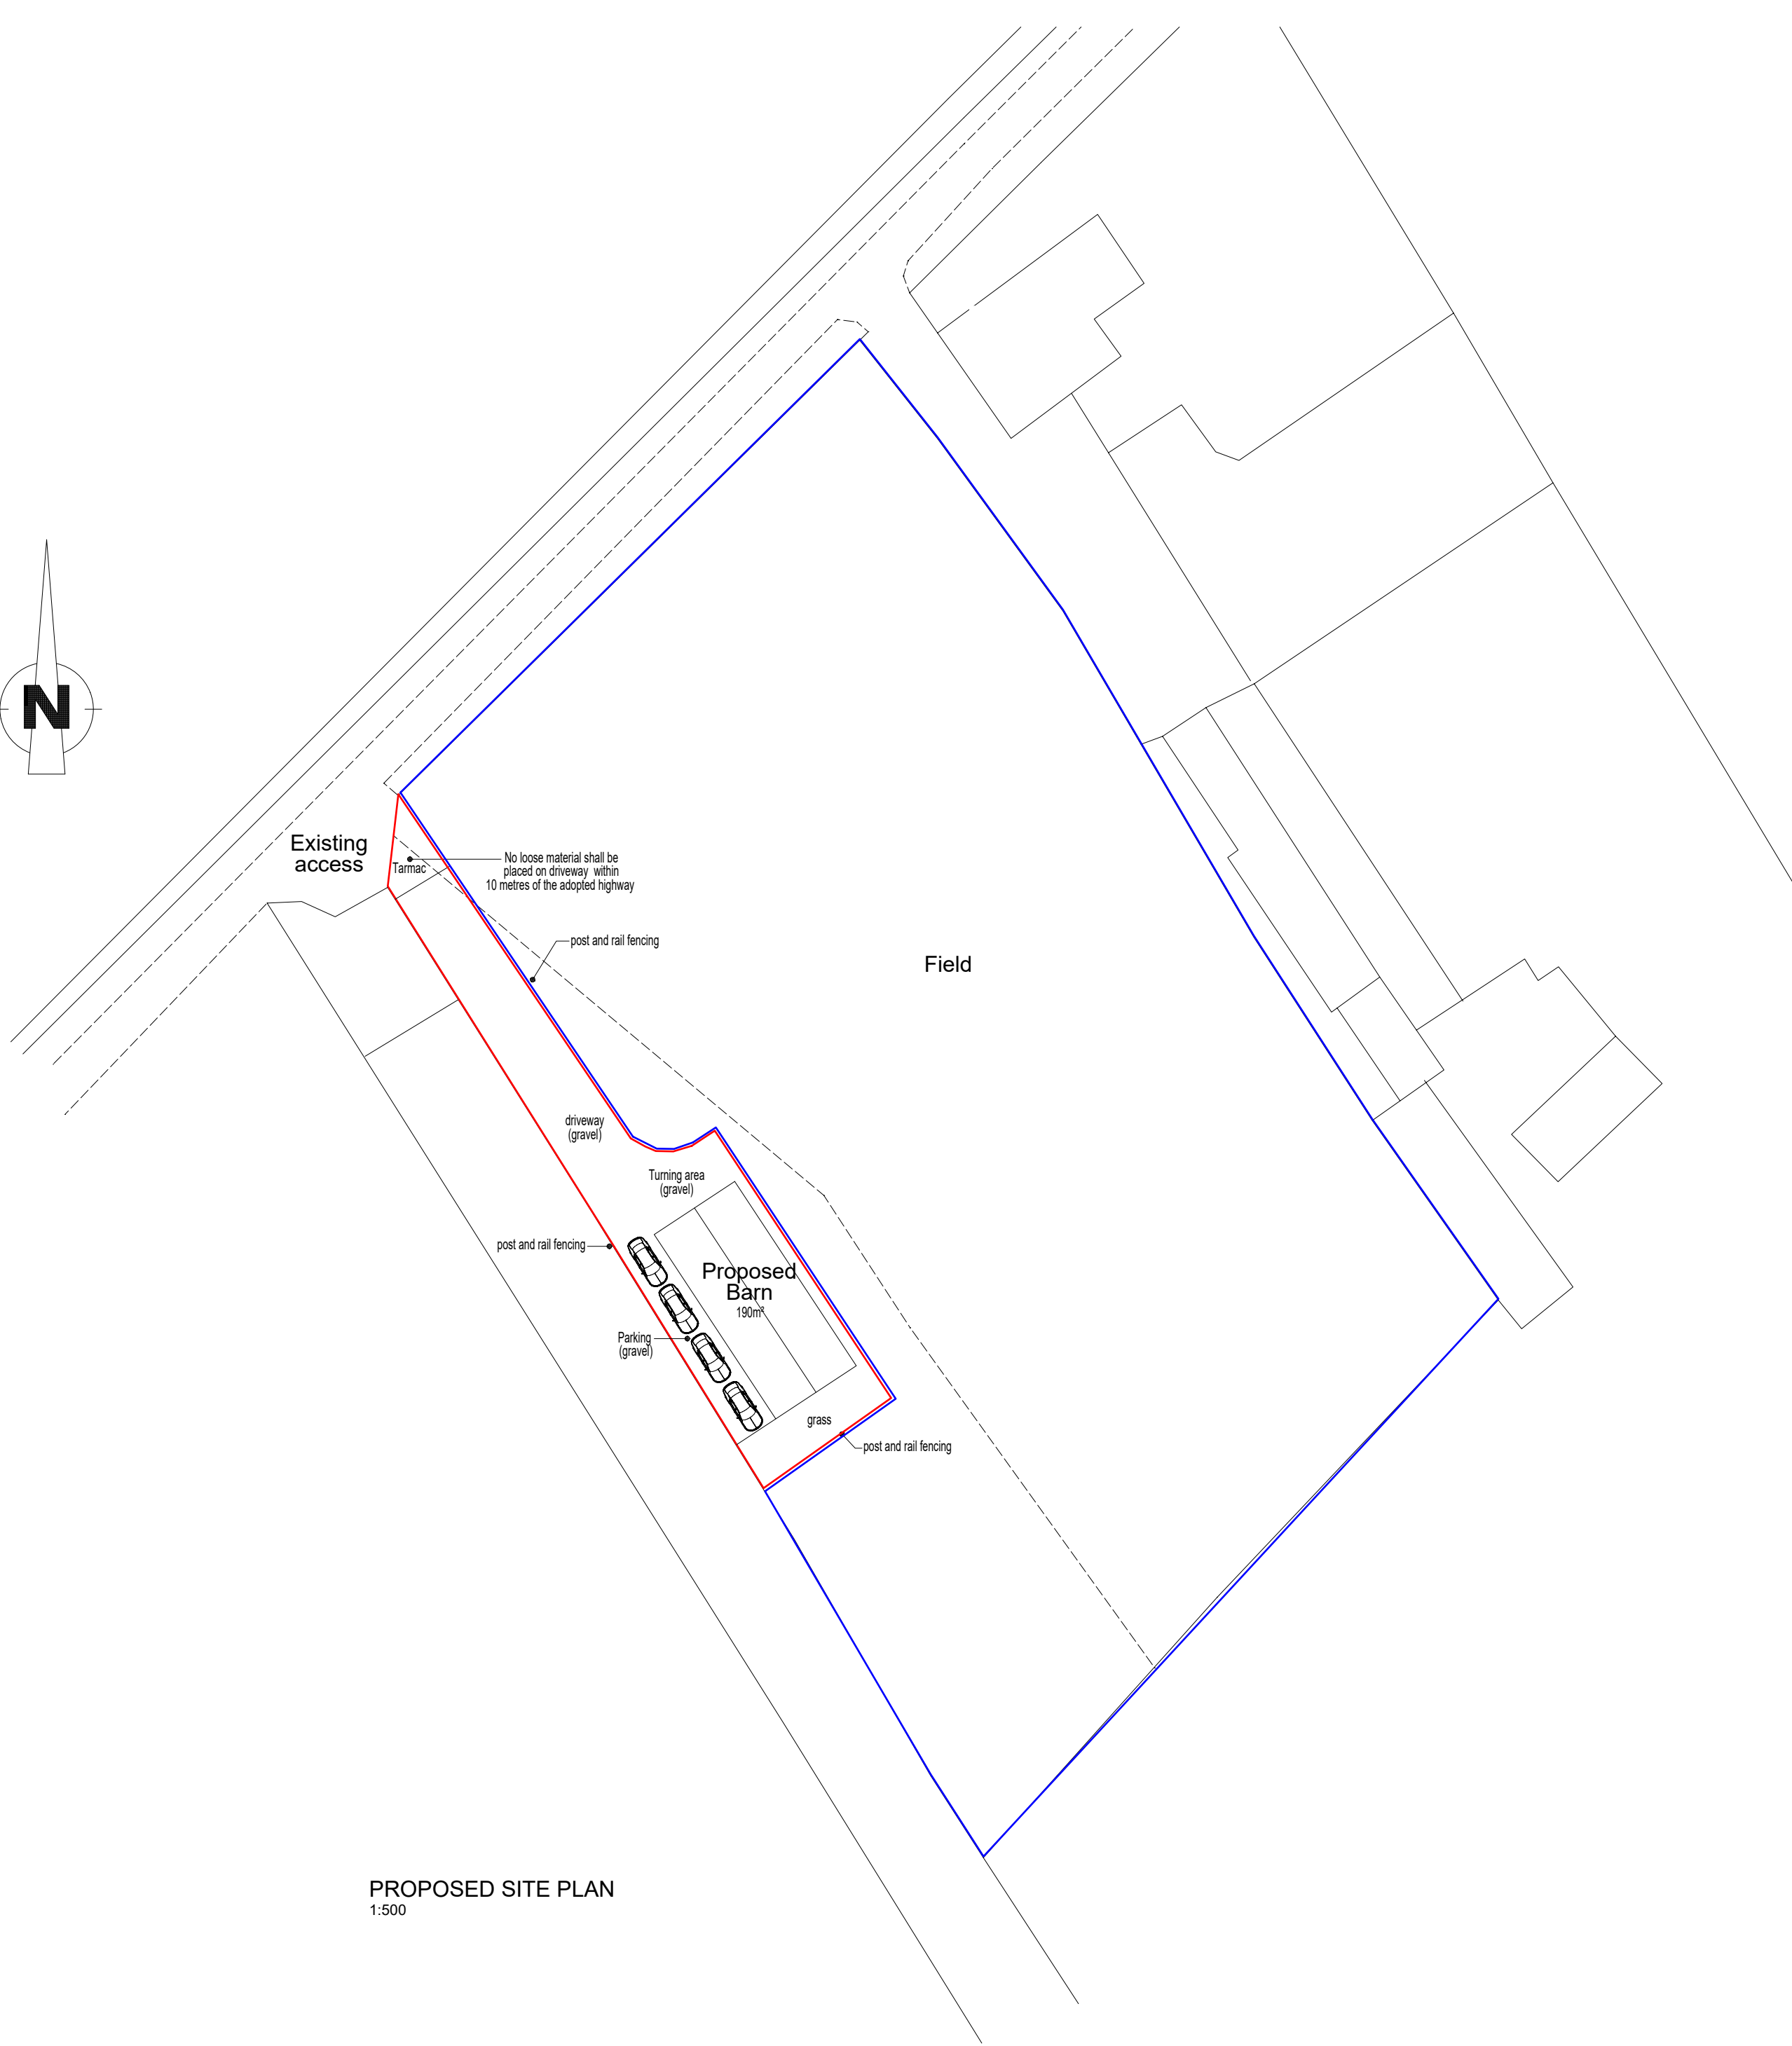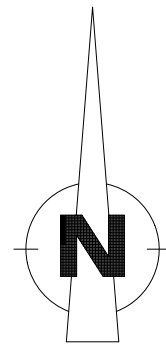

PROPOSED SITE PLAN
1:500

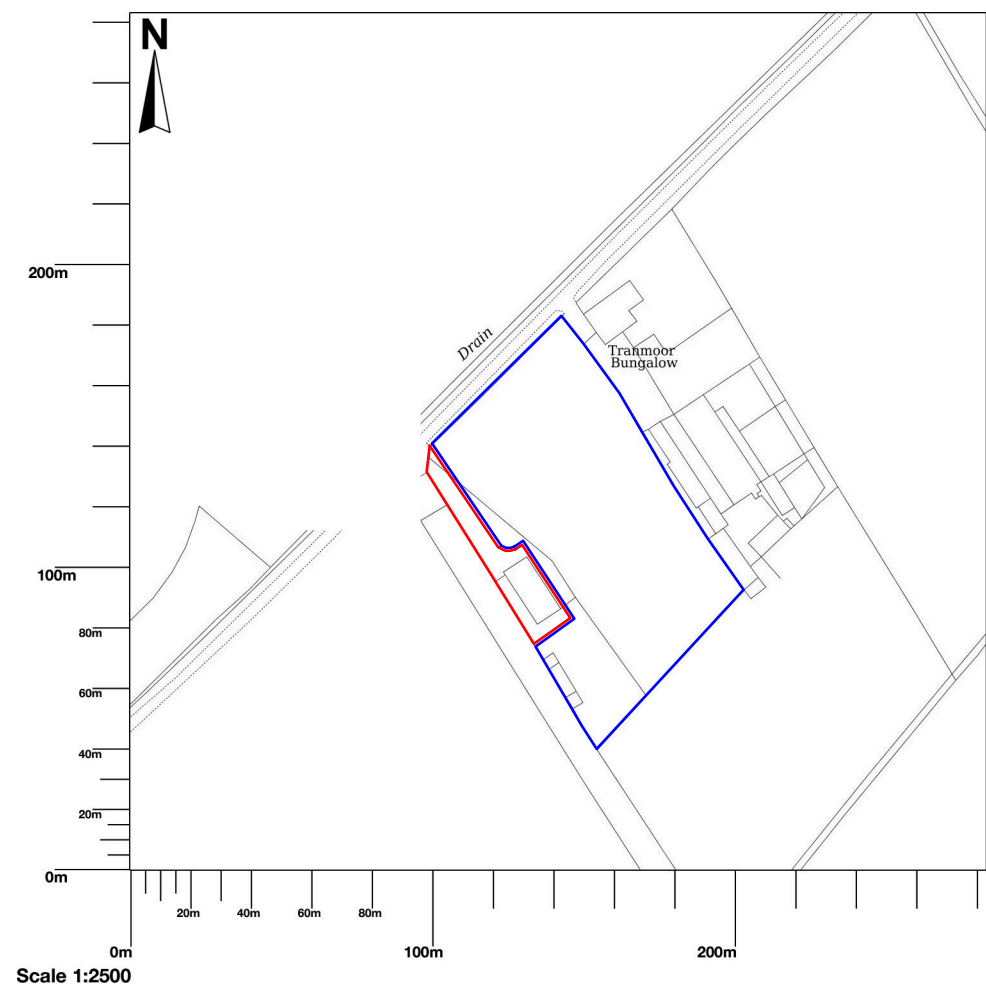

LOCATION PLAN
1:2500

from the OS National Geographic Database. Reproduction
copyright 2022. Supplied by UKPlanningMaps.com a

- Title:
- PROPOSED PLANS AND ELEVATIONS

Scale 1:100 @ A1	Date 08-2025	Drawn DS
Drawing		
A B C D E F G H J		