


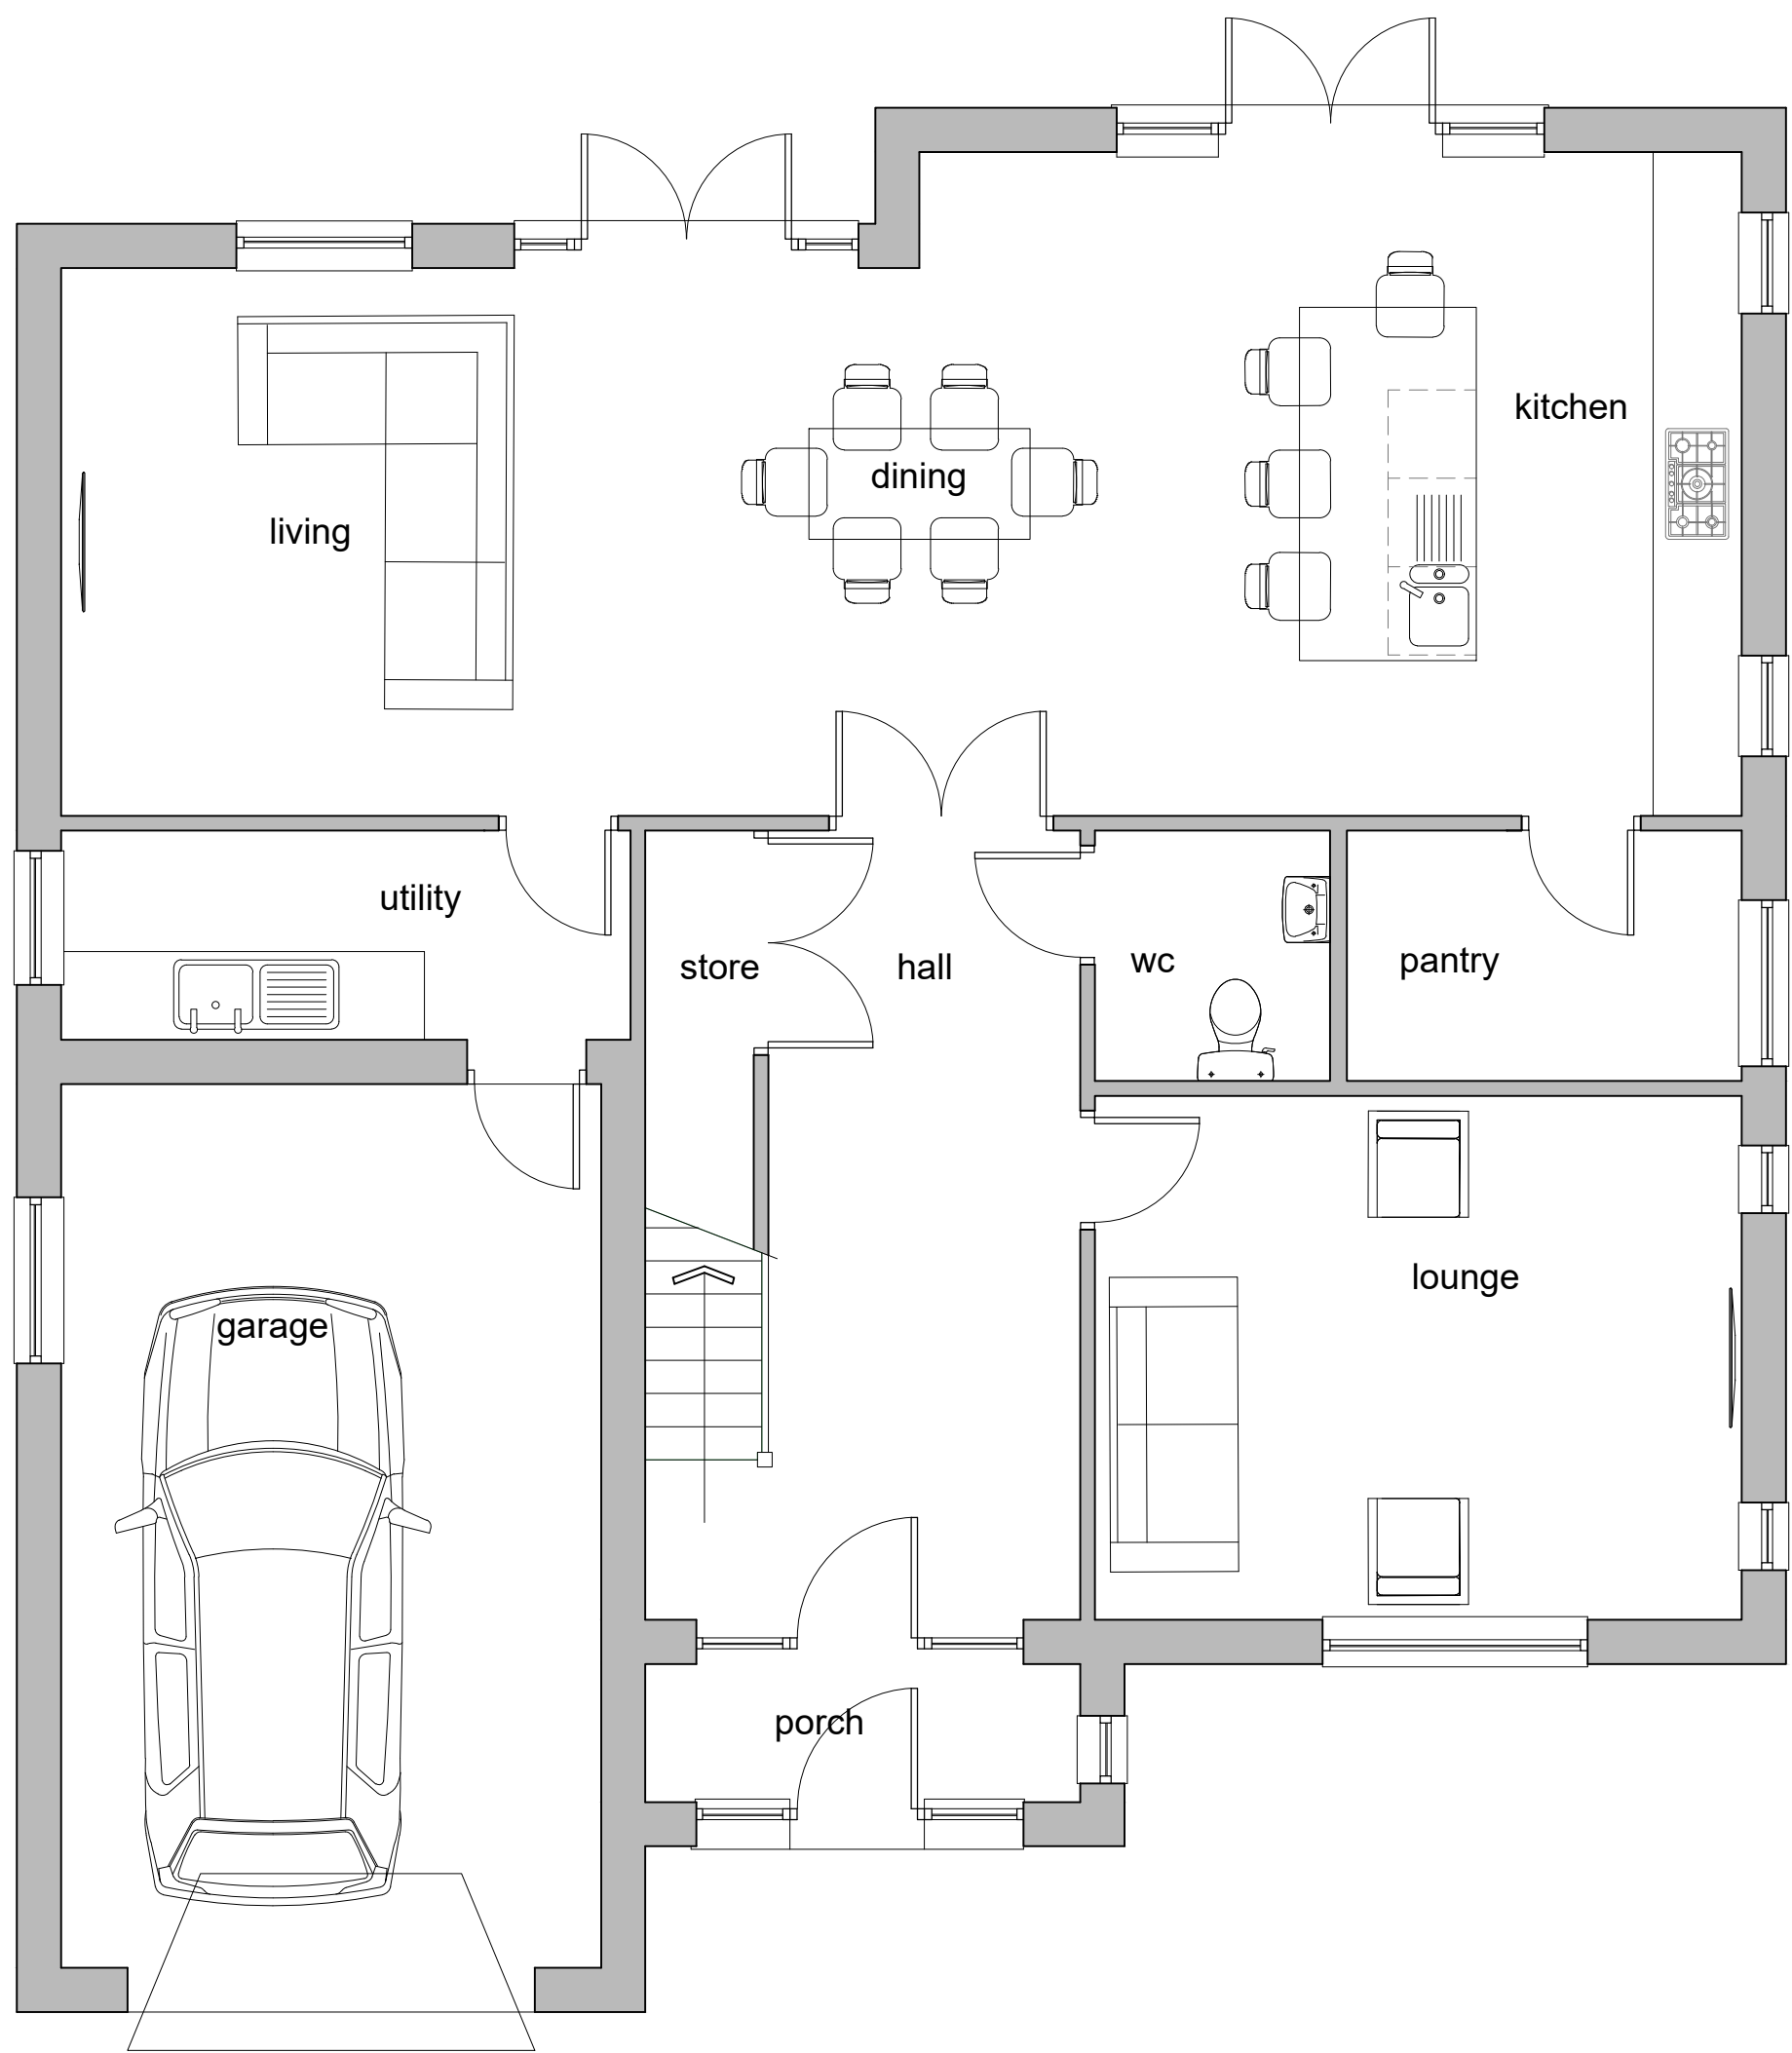
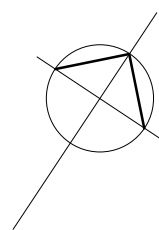


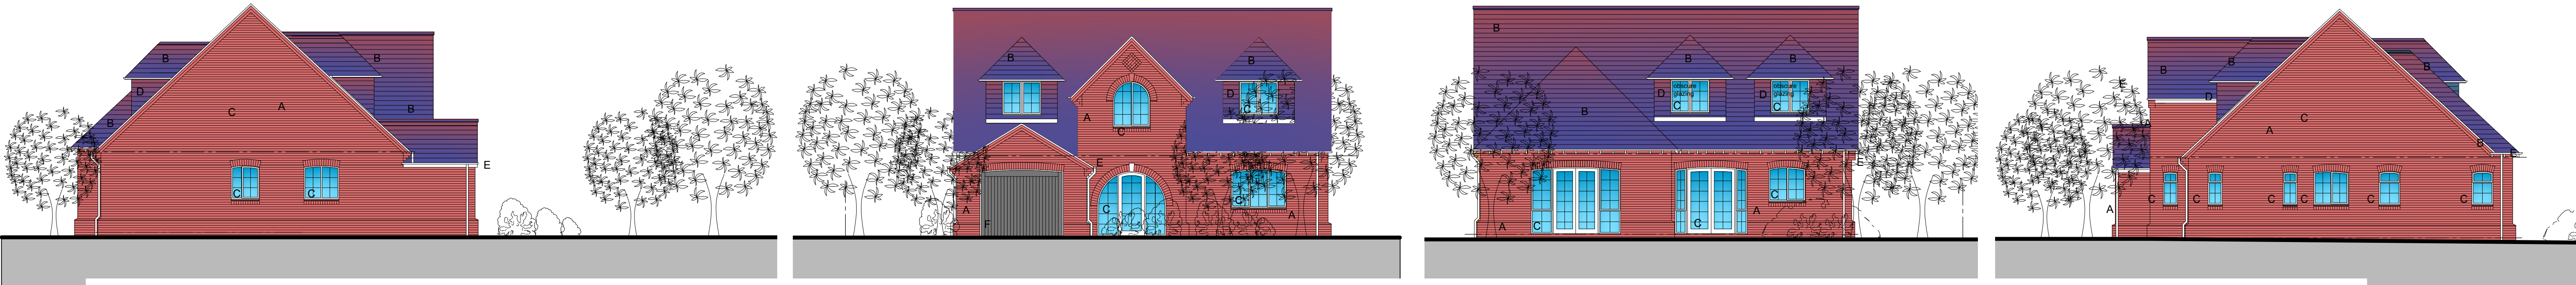

0 proposed ground floor plan
Scale: 1:50

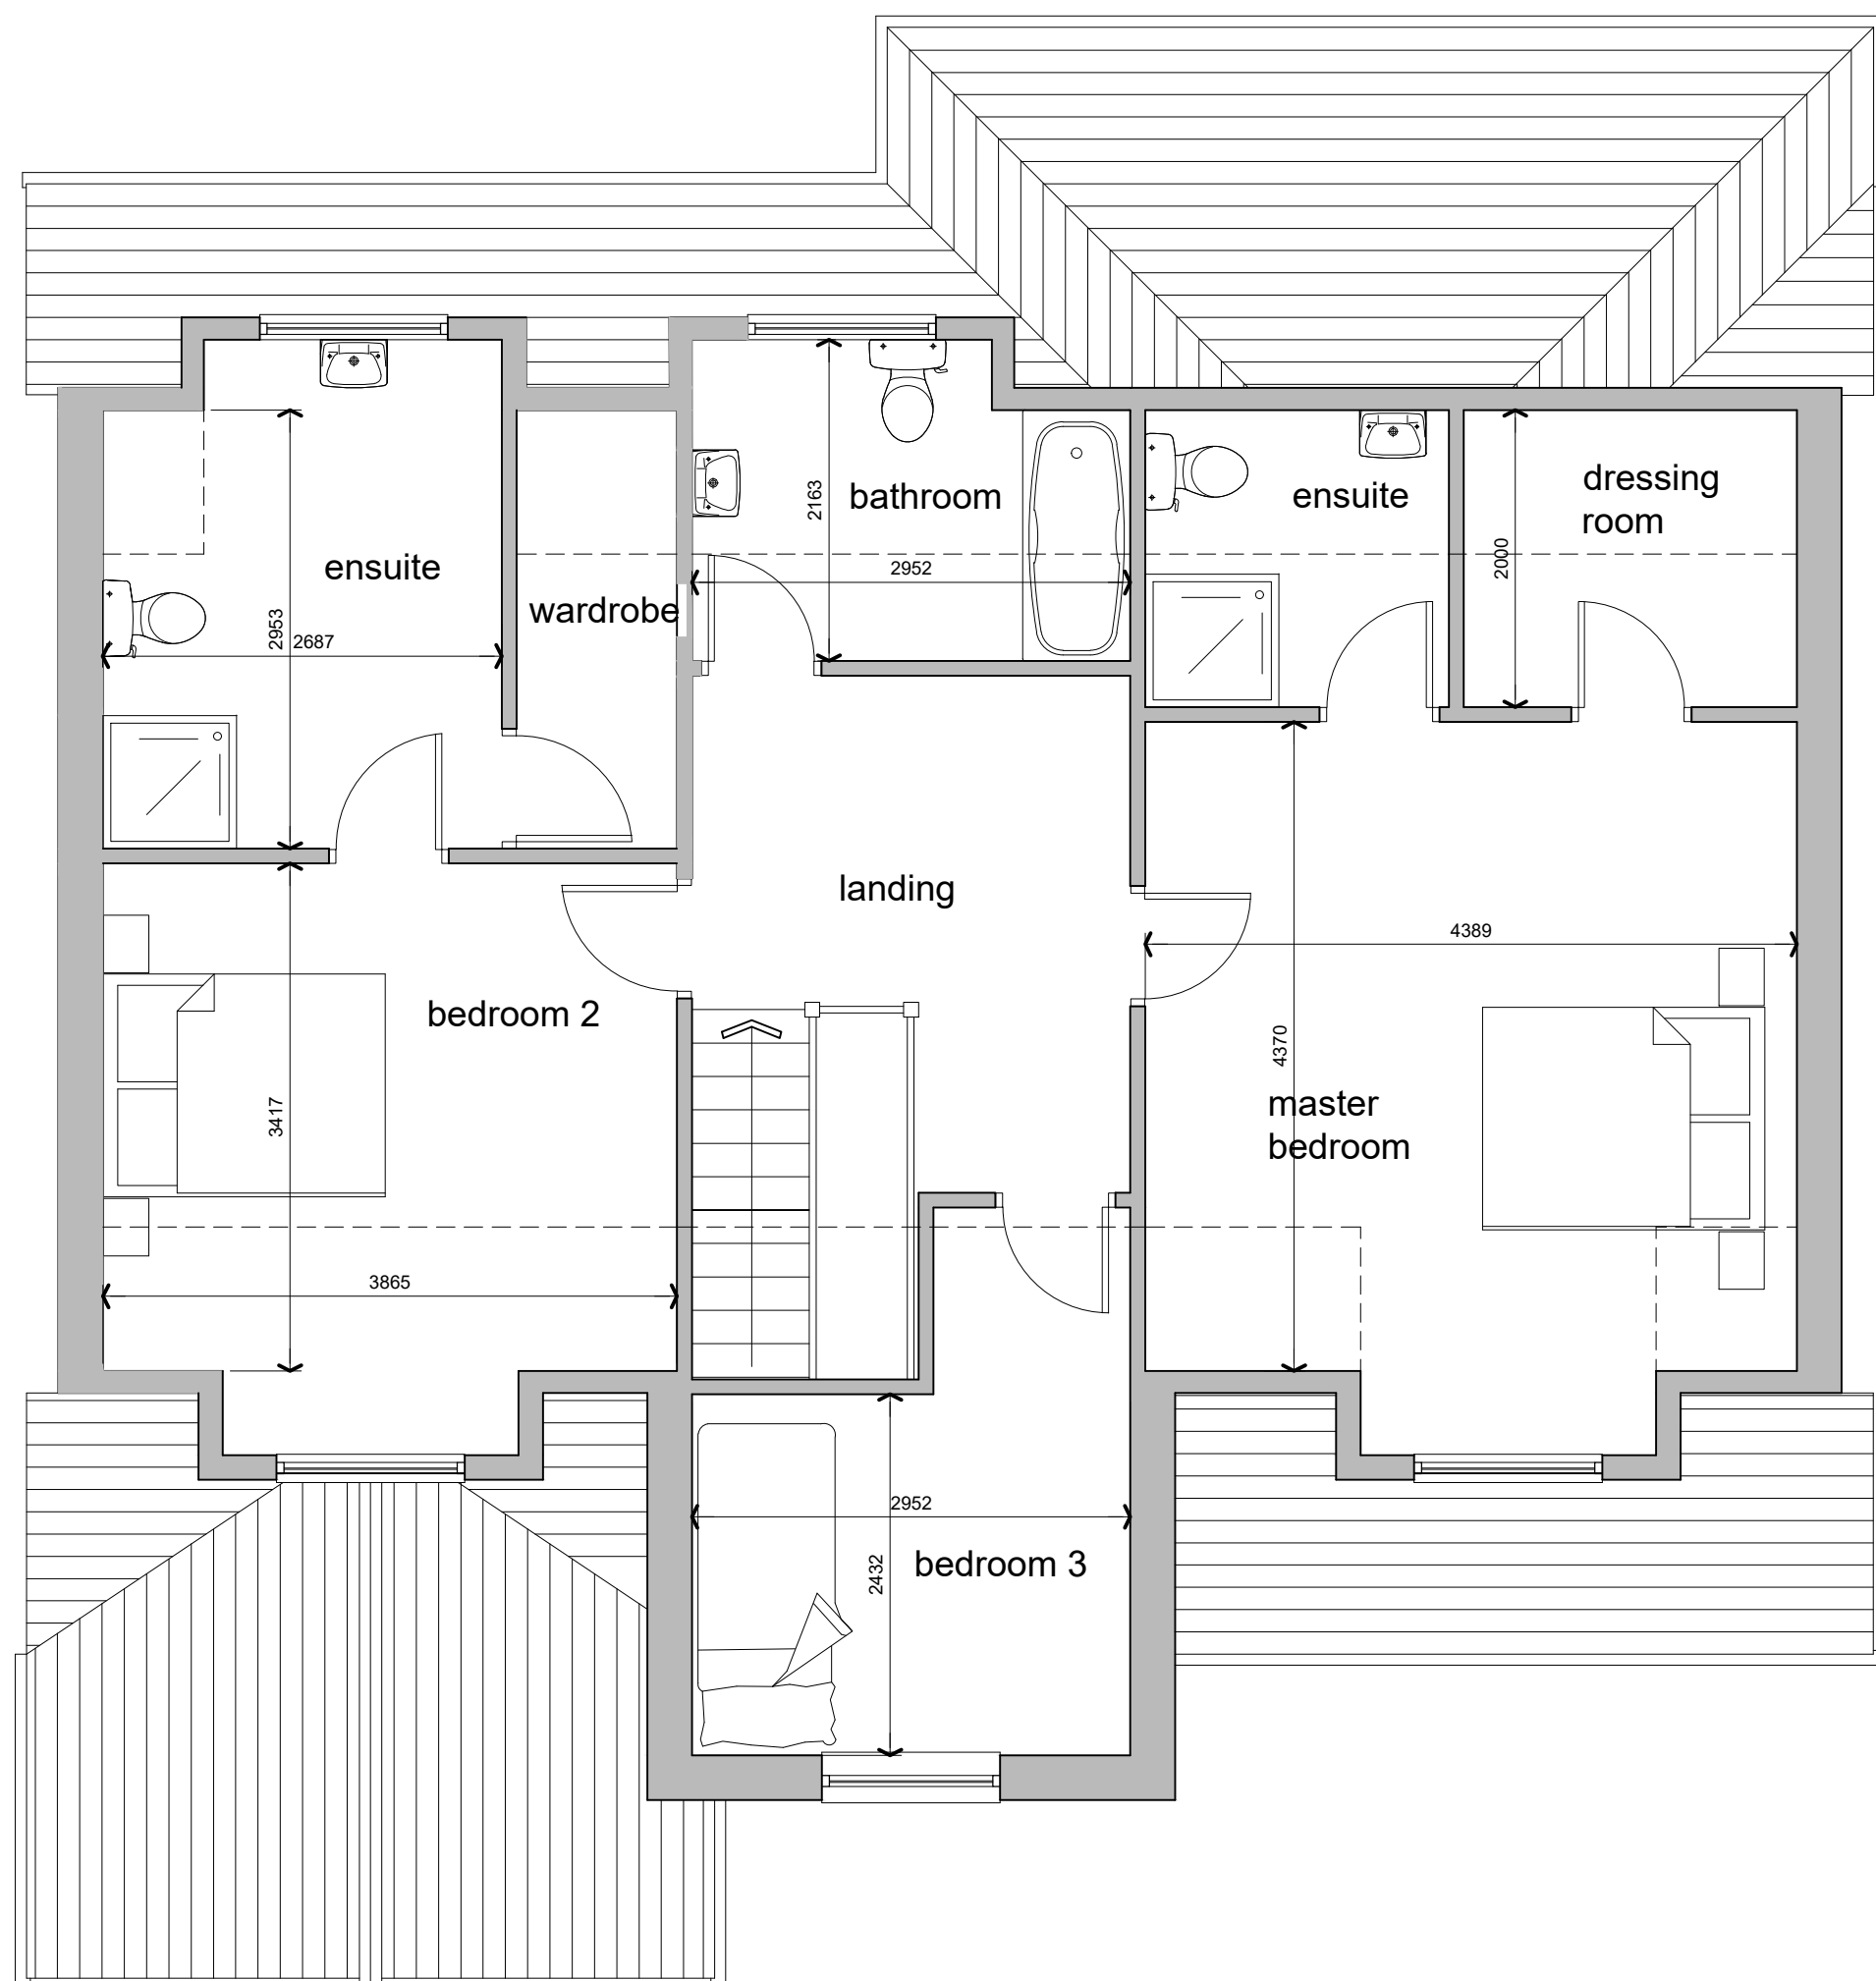

1 proposed first floor plan
Scale: 1:50

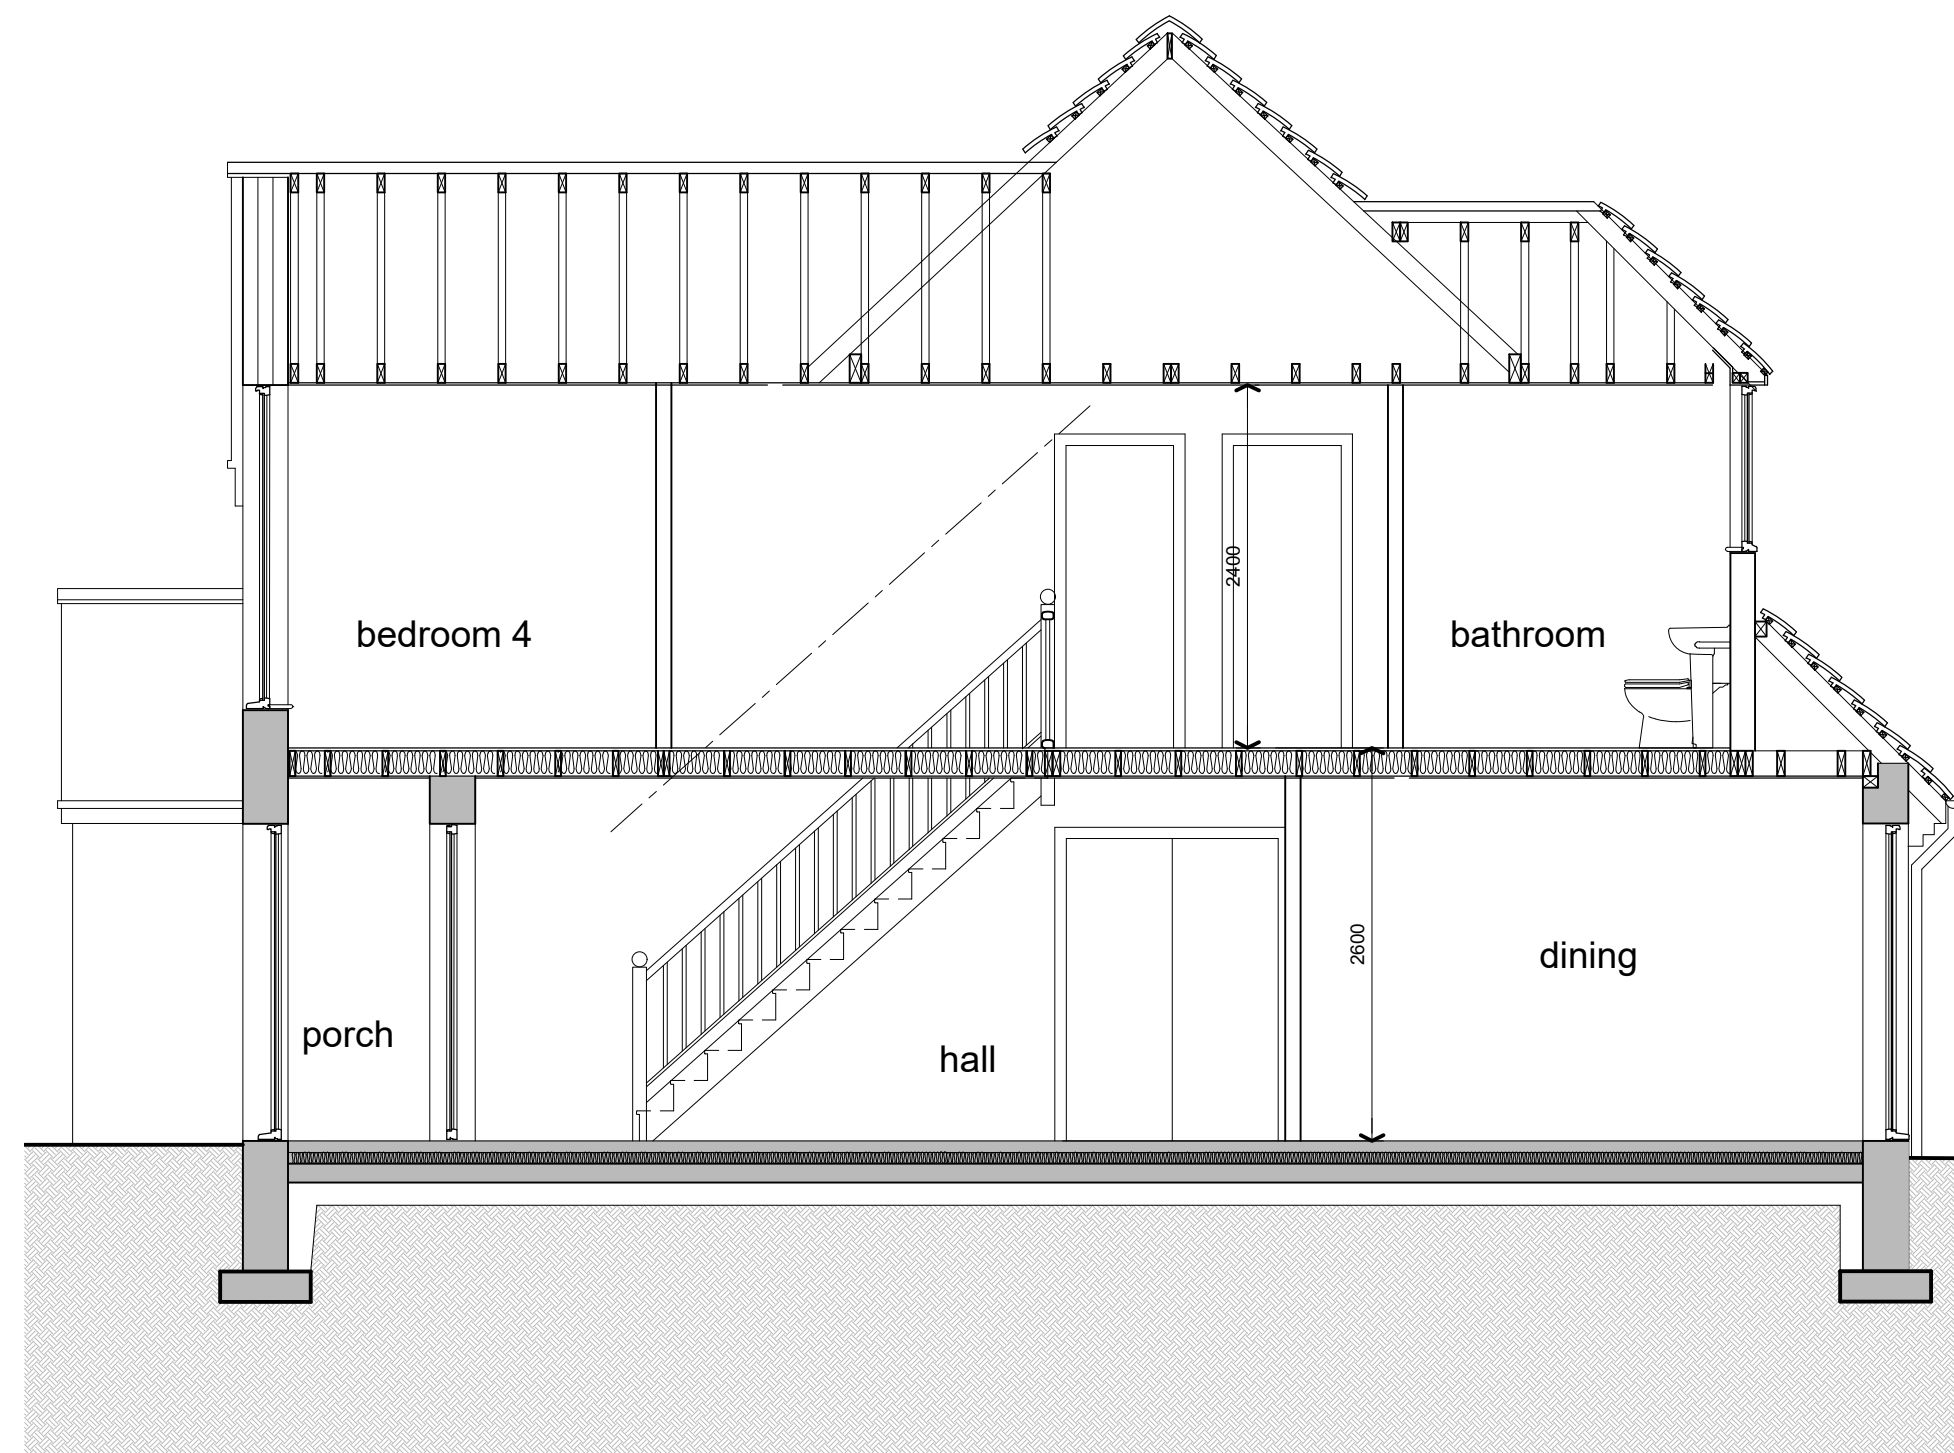

a proposed section
Scale: 1:50

KEY TO MATERIALS

- A facing brickwork - wienerberger kempley antique buff
B clay 'Rosemary' roof tiles - blue brindle
C black wood grain PVC double glazed windows and doors - obscured glass as required
D clay 'Rosemary' vertical tiles - blue brindle
E sprocketed eaves detail and black PVC eaves gutter and rwps
F black wood grain steel 'up & over' garage door

Space requirements for compliance with Technical housing standards - nationally described space standards 2015

GROSS INTERNAL AREAS

3 bed 5 person Proposed - 205.96m² Minimum Required - 84m²

ROOM AREAS SCHEDULE

	MIN INTERNAL AREA	ACTUAL AREA	MIN WIDTH	ACTUAL WIDTH
Bedroom 1	11.5m²	20.50m²	2.75m	4.38m
Bedroom 2	11.5m²	13.20m²	2.75m	3.41m
Bedroom 3	7.5m²	8.84m²	2.15m	2.43m

PLANNING

SUBJECT

DRAWN

CHECKED

SCALE: 1:50 1:100 @ A1

JOB No.

DWG No.

AMENDMENT