




EXISTING GRPUND FLOOR PLAN 1:50@A2

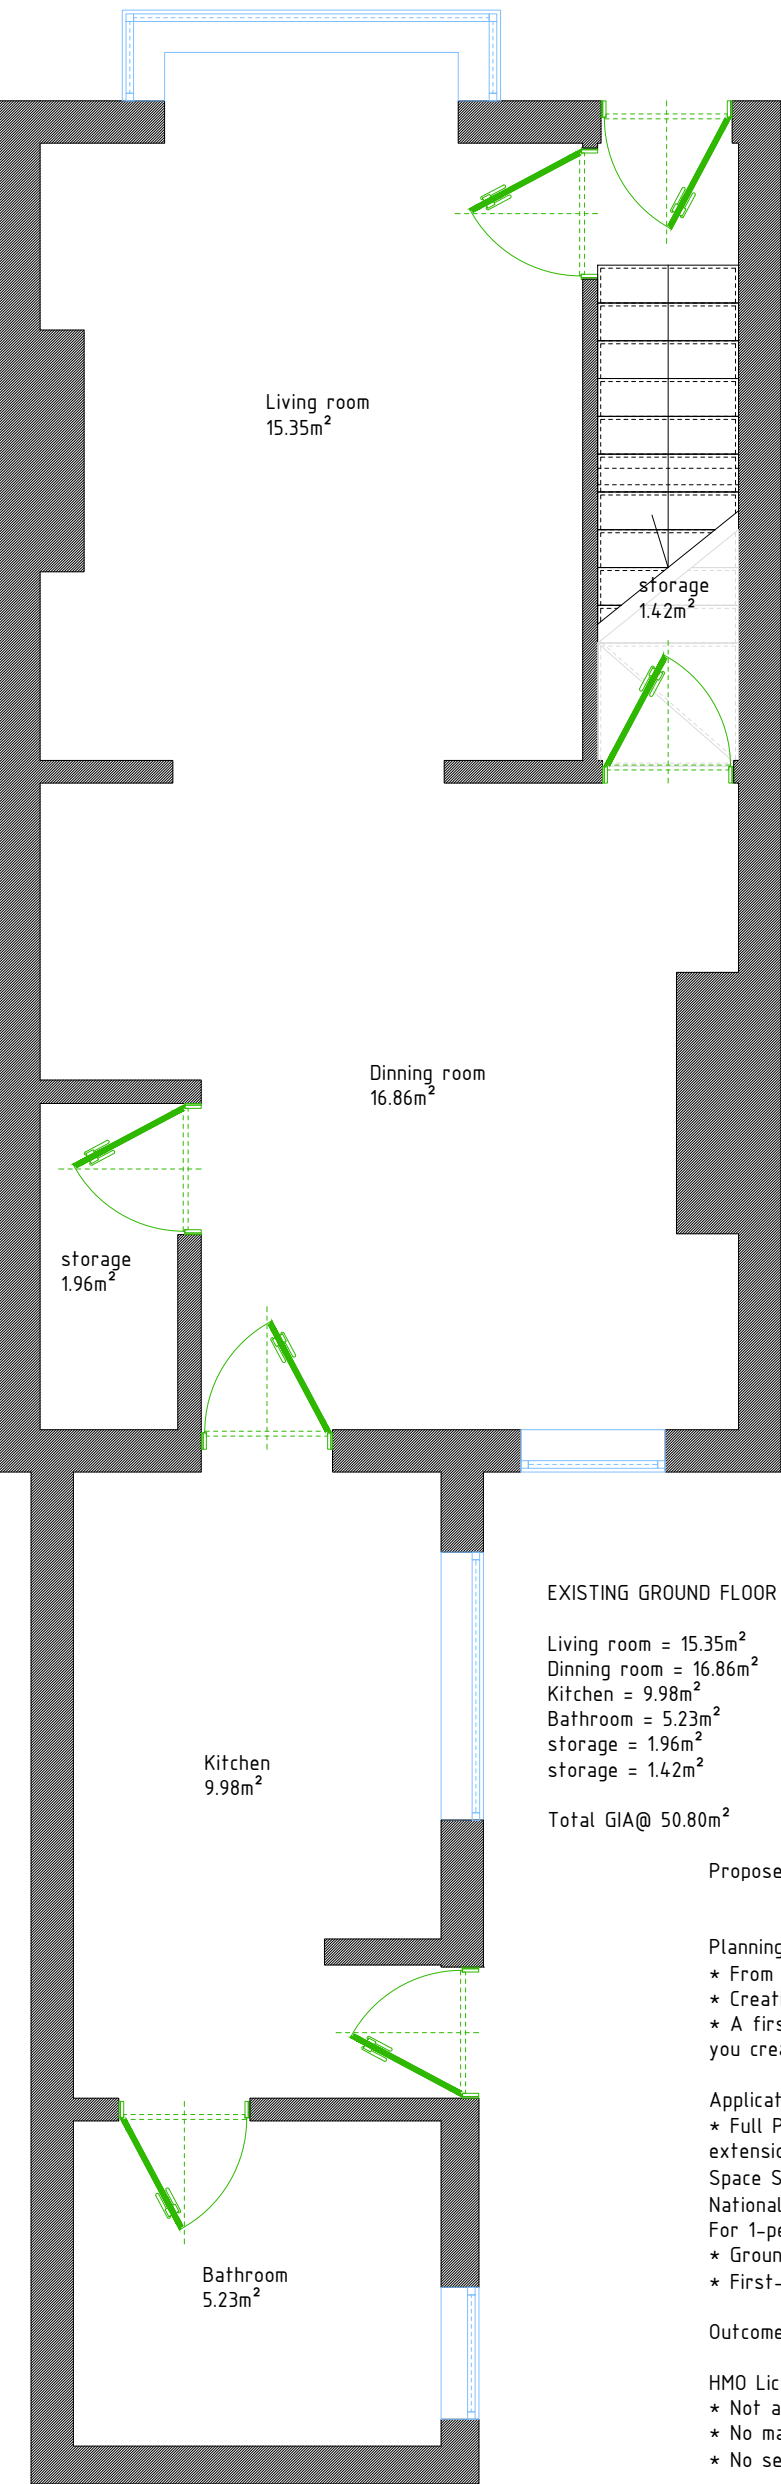


EXISTING FIRST FLOOR PLAN 1:50@A2

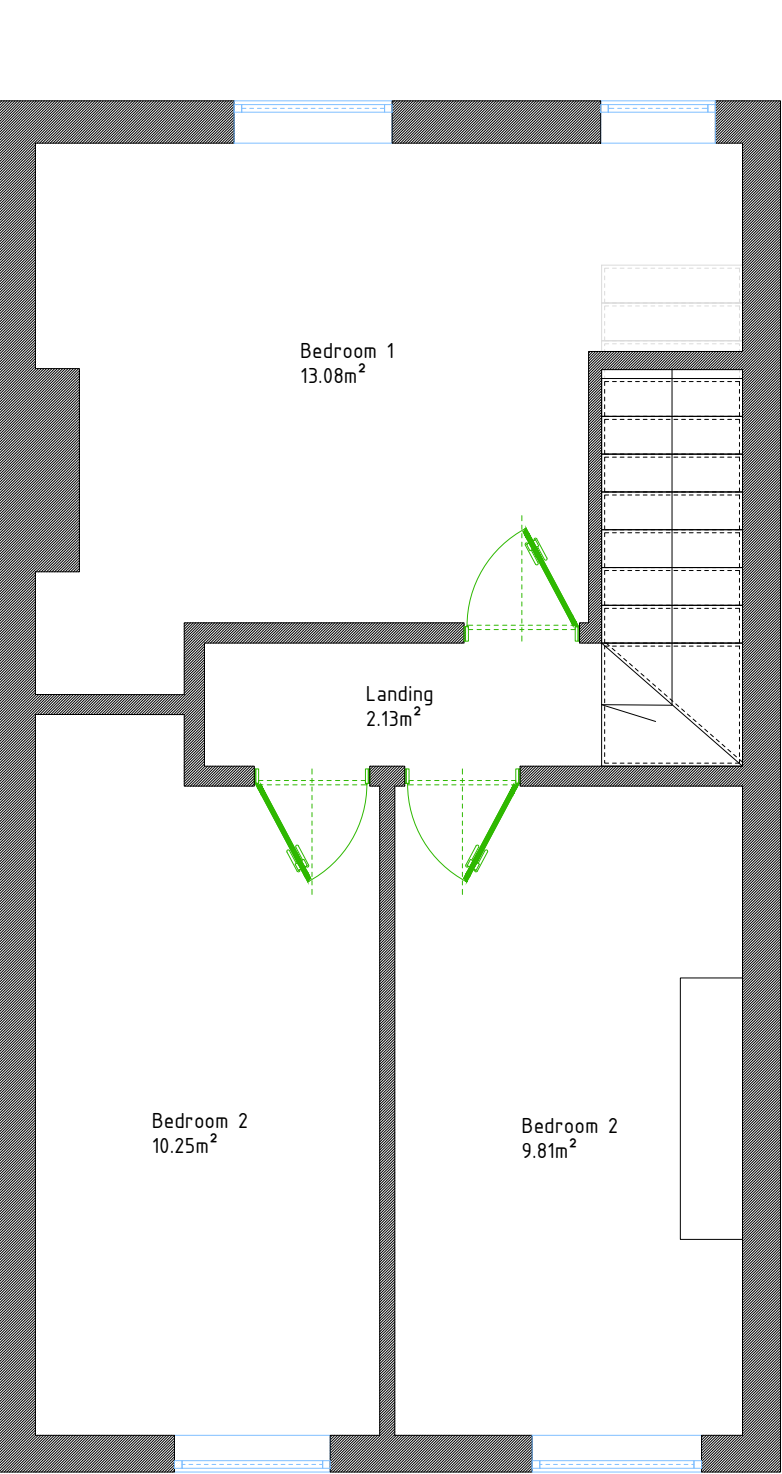

BB PROPOSED GRPUND FLOOR PLAN 1:50@A2

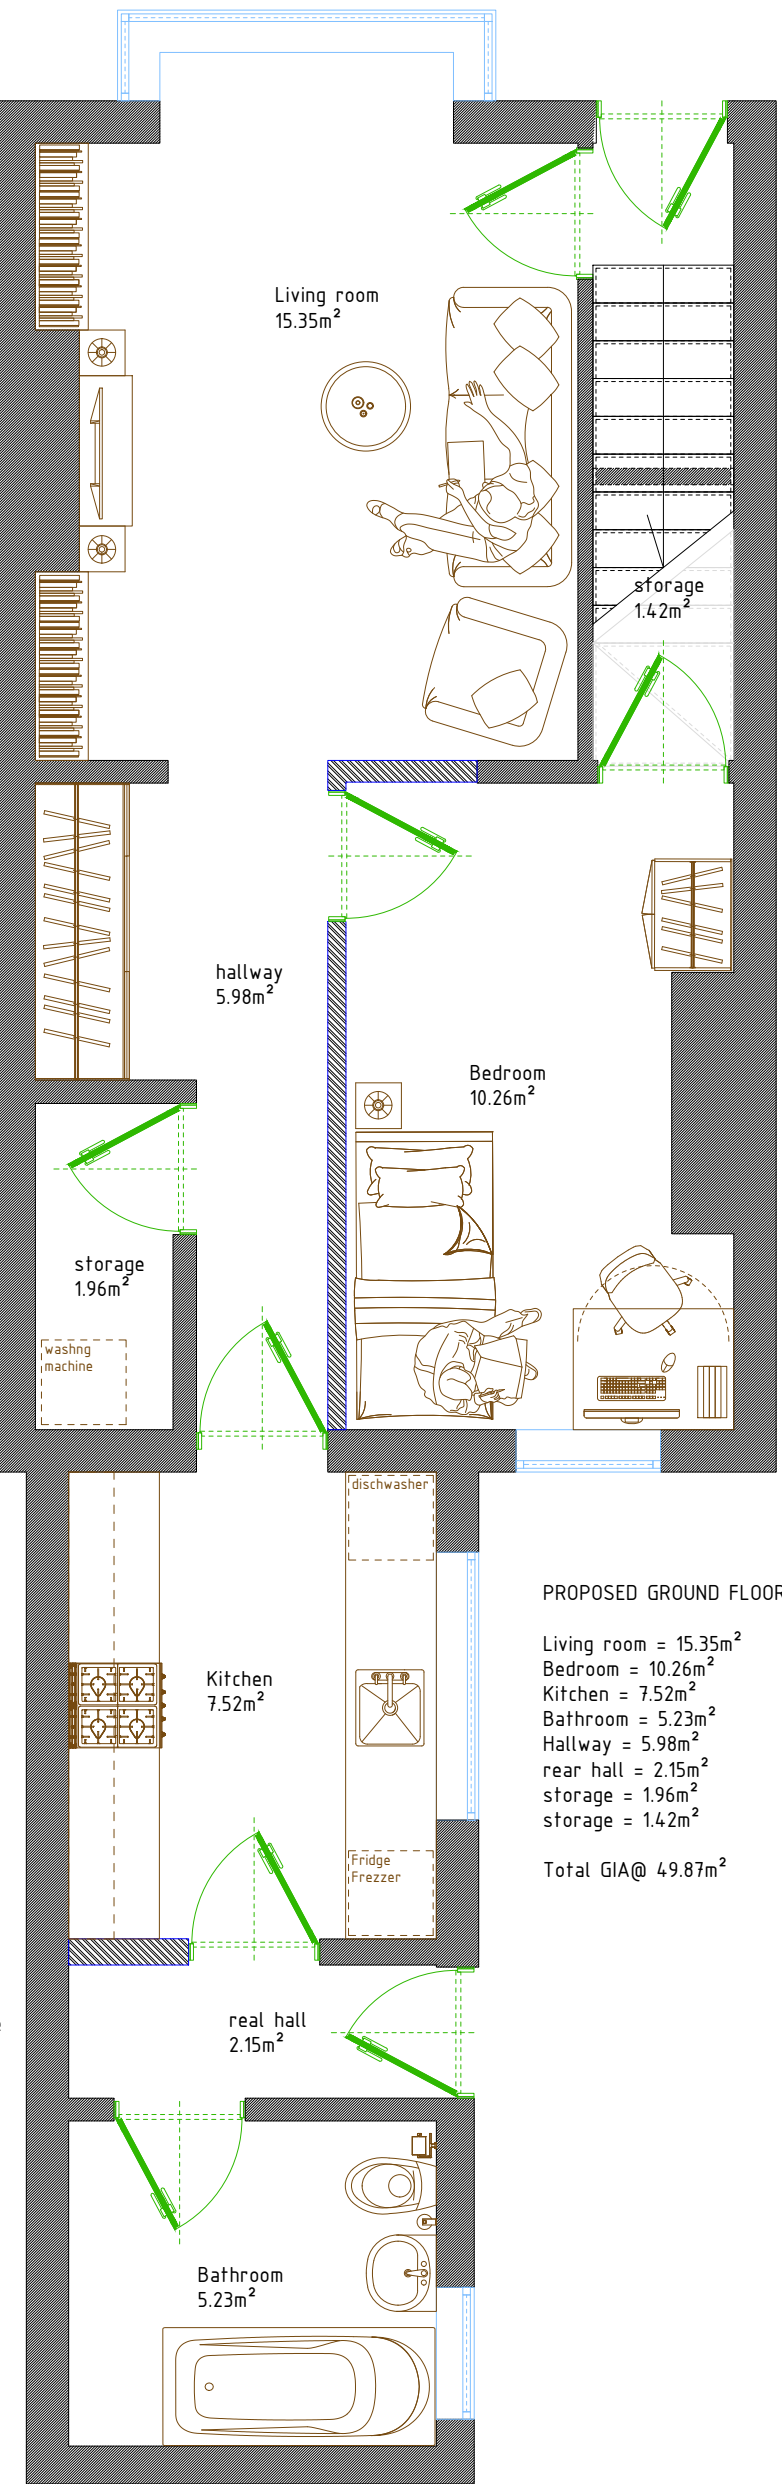

BB EXISTING FIRST FLOOR PLAN 1:50@A2

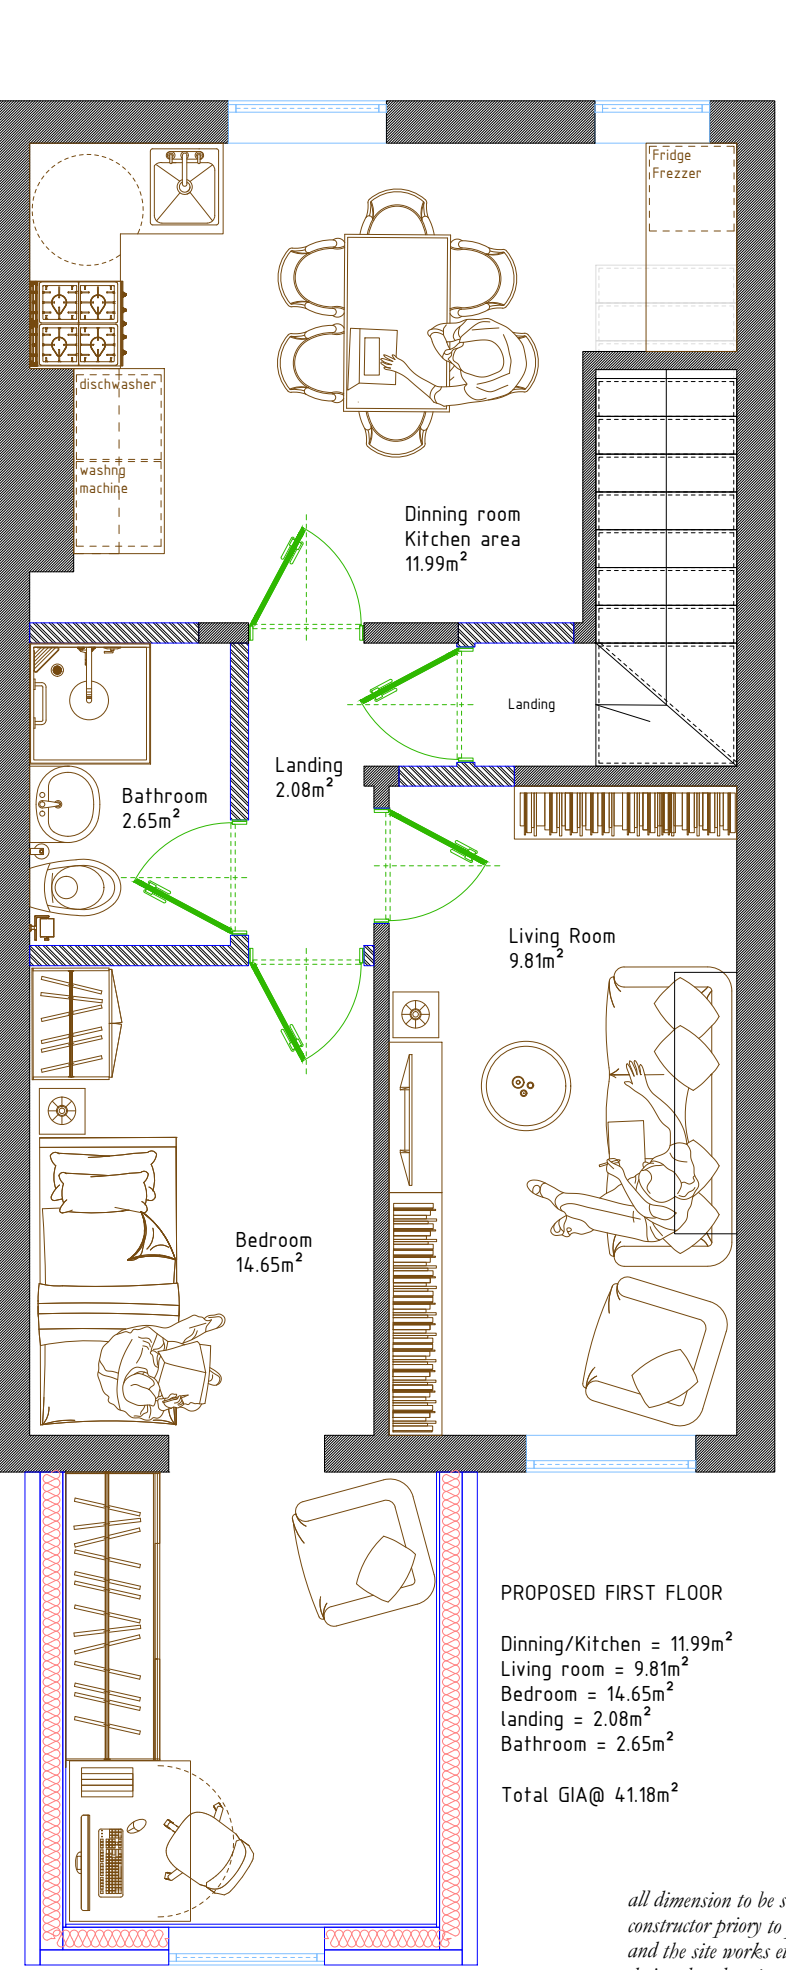

EXISTING GROUND FLOOR

Living room = 15.35m²
Dinning room = 16.86m²
Kitchen = 9.98m²
Bathroom = 5.23m²
storage = 1.96m²
storage = 1.42m²

Total GIA@ 50.80m²

Proposed PLAN – Two Self-Contained Flats + First-Floor Rear Extension

Planning Permission Required

- * From one dwelling (C3) to two self-contained dwellings (2 x C3).
- * Creating additional dwellings is always a material change.
- * A first-floor rear extension falls outside permitted development for flat conversions, and, in any event, PD rights do not apply once you create flats.

Application type:

- * Full Planning Application: "Change of use from a single dwellinghouse (C3) to two self-contained flats (C3) with a first-floor rear extension."

Space Standards (Key Planning Risk Resolved)

Nationally Described Space Standards (NDSS)

For 1-person, 1-bed flats: minimum 37 m² GIA.

- * Ground-floor flat: ~49.9 m² → compliant

- * First-floor flat (with extension): ~41.2 m² → compliant

Outcome: The BB scheme addresses the principal refusal risk present in the AA scheme by lifting the upper flat above NDSS.

HMO Licensing

- * Not an HMO under the Housing Act 2004.
- * No mandatory HMO licence.
- * No selective licensing triggered for self-contained flats (even if an area scheme existed).

Building Regulations – REQUIRED (Full Plans)

Flat conversions with extensions are more onerous than HMOs.

Other Planning Matters Officers Will Assess

- * Design & Amenity: Scale/massing of the rear extension; impact on neighbours (overlooking/overshadowing).
- * Refuse & Recycling: Provision for two households with accessible bin storage.
- * Parking: DN4 standards; 1-person flats often accepted with low provision, but must be justified.
- * Flood Risk: Minor development + extension; your existing flood note/FRA principles remain applicable.

EXISTING FIRST FLOOR

Bedroom 1 = 13.08m²
Bedroom 2 = 10.25m²
Bedroom 3 = 9.81m²
landing = 2.13m²

Total GIA@ 35.27m²

PROPOSED GROUND FLOOR

Living room = 15.35m²
Bedroom = 10.26m²
Kitchen = 7.52m²
Bathroom = 5.23m²
Hallway = 5.98m²
rear hall = 2.15m²
storage = 1.96m²
storage = 1.42m²

Total GIA@ 49.87m²

PROPOSED FIRST FLOOR

Dining/Kitchen = 11.99m²
Living room = 9.81m²
Bedroom = 14.65m²
landing = 2.08m²
Bathroom = 2.65m²

Total GIA@ 41.18m²

all dimension to be site checked by the constructor prior to procuring the materials and the site works etc. Temporary props to be designed and maintained by the contractor.



This drawing shall be checked and verified by the contractor prior to commencement of works on site. Any discrepancy, inconsistency, or query identified shall be reported immediately to the designer and resolved before proceeding with construction. No work shall be undertaken based on assumptions or unverified information.	
DRAWING DESCRIPTION: Existing and Proposed Floor plan Flat conversion	
SITE:	
CLIENT:	
DATE:	
SCALE:	
These drawings are intended exclusively for use by authorised individuals and in this project. This design remains the copyright of the designer. No part of this drawing or associated information may be altered, copied, or reused without the written consent of the designer. Any proposed changes shall be referred to and agreed upon with the designer before implementation. Contractors and site operatives must verify that all work is carried out in accordance with the approved drawings, relevant standards, and applicable health and safety regulations. All dimensions and levels shall be verified on site before fabrication, procurement, and construction, serving as a control point to ensure accuracy. The designer accepts no responsibility for works that are installed incorrectly, unsafely, or not in accordance with the issued information. These drawings have been produced solely for Planning application submission and shall not be used for any other purposes. The drawings may be subject to amendment during the statutory approval process, which typically follows a standard timeline. Any surveyed or measured information shown on the drawings is indicated and cannot be guaranteed to be unless confirmed by a third-party check on site.	